

THESE PLANS WERE PREPARED BY A BUILDING DESIGNER, NOT AN ENGINEER. ALL STRUCTURAL ASPECTS OF THE FOUNDATION ARE TO BE DESIGNED BY OTHERS. THE DESIGNER WILL NOT BE HELD RESPONSIBLE FOR THE STRUCTURAL DESIGN IN ANY WAY OR ANY PROBLEMS WHICH MAY ARISE.

DO NOT SCALE PLANS! SOME DEVIATION FROM SCALE MAY OCCUR AS A RESULT OF REPRODUCTION. CONTRACTOR TO VERIFY ALL DIMENSIONS PRIOR TO CONSTRUCTION.

THE BUILDER SHALL CONFIRM THAT THESE PLANS MEET THE BUILDING CODES, ZONING ORDINANCES, RESTRICTIVE COVENANTS, AND/OR OTHER REGULATIONS IN THE LOCALITY WHERE THE PROJECT IS BEING BUILT.

ALL WRITTEN NOTES ON THESE DRAWINGS SHALL TAKE
PRECEDENCE OVER THE MINIMUM STANDARD NOTES
DETAILED ON SHEET D1 OF THESE DRAWINGS.

ALL MATERIALS AND PRODUCTS ARE TO BE INSTALLED
ACCORDING TO THE MANUFACTURER'S SPECIFICATIONS.

CEILING HEIGHTS TAKEN FROM WHERE THE NOTE IS LOCATED
ON THE PLAN.

ALL FLOOR DRAINS TO HAVE OVERFLOW PAN WITH RELIEF
LINE TO OUTSIDE OR STORM SEWER.

PROVIDE PLUMBING ACCESS PANEL AT ALL BATH TUBS PER
SECTION P2704.1.

ALL GLASS AT TUBS AND SHOWERS SHALL BE TEMPERED SAFETY GLASS AND MUST COMPLY WITH SECTION R308.4

SEE STAIR NOTES - SHEET D1, COMPLY WITH SECTION R311.5

PROVIDE PULL DOWN ATTIC STAIR WITH A MINIMUM OPENING WIDTH OF NOT LESS THAN 22' (BETWEEN HARDWARE A LOAD CAPACITY OF NOT LESS THAN 350 lbs. PROVIDE MINIMUM HEAD CLEARANCE OF 30'. SEE SECTIONS R807 AND M1305.13

LOCATE WATER HEATER(S) IN ATTIC (U.N.O.) ABOVE A LOAD BEARING PARTITION IN A PAN WITH A RELIEF LINE TO OUTSIDE. INSTALLATION TO COMPLY WITH SECTIONS F2801, F2802 AND F2803

LOCATE H.V.A.C. EQUIPMENT IN ATTIC (U.N.O.).

PROVIDE 24" WIDE PLYWOOD WALKWAY TO ACCESS ALL MECHANICAL EQUIPMENT LOCATED IN ATTIC. MAXIMUM DISTANCE FROM ATTIC ACCESS TO EQUIPMENT SHALL NOT EXCEED 20'-0". PROVIDE A 30' WIDE SERVICE PLATFORM A SERVICE SIDE OF ALL EQUIPMENT IN ATTIC.

ALL INSULATION SHALL HAVE A FLAME SPREAD RATING NOT TO EXCEED 25 AND A SMOKE DENSITY RATING NOT TO EXCEED 450. SEE SECTION R316

PROVIDE ADEQUATE FURRING SO VENT AND SOIL PIPES DO NOT PENETRATE PLATES. ALL PLUMBING VENTS SHALL EXIT THROUGH A ROOF PLANE THAT SLOPES TO THE BACK.

FINISHED GRADING SHALL PROVIDE POSITIVE DRAINAGE AT ALL TIMES.

ALL EXTERIOR WALLS, HOUSE TO GARAGE WALLS, AND CEILINGS ARE TO HAVE INSULATION PER BUILDER'S SPECIFICATIONS.

ALL STRUCTURAL FRAMING LUMBER AND MATERIALS SHALL HAVE THE MINIMUM ALLOWABLE UNIT STRESS REQUIRED BY THE LOCAL BUILDING CODE. ALL STRUCTURAL MEMBERS SHALL COMPLY WITH THE DESIGN LOADS, SPANS, SPACING, AND GRADING AS SPECIFIED BY THE LOCAL BUILDING CODE. ALL STRUCTURAL MEMBERS SHALL BE FRAMED, ANCHORED, TIED, AND BRACED AS TO DEVELOP THE STRENGTH AND RIGIDITY NECESSARY FOR THE PURPOSE IN WHICH THEY ARE BEING USED.

ALL LUMBER IN CONTACT WITH CONCRETE SHALL BE
PRESSURE TREATED LUMBER.

DO NO CUTTING, DRILLING, OR MODIFYING OF STRUCTURAL
MEMBERS WITHOUT PROPER APPROVAL FROM ENGINEER OF
RECORD.

ALL MECHANICAL CONTRACTORS (ELECTRICAL, PLUMBING, AND HVAC) SHALL CONFORM TO ALL NATIONAL, STATE, AND LOCAL CODES. CONTRACTORS SHALL VERIFY AND CONFIRM THE LOCATIONS OF ALL MECHANICAL DEVICES WITH THE BUILDER PRIOR TO INSTALLATION.

THESE DRAWINGS AND THE DESIGN ARE THE SOLE PROPER
OF DCA DESIGN LLC AND MAY NOT BE USED IN WHOLE OR
PART WITHOUT WRITTEN PERMISSION.



RENDERING VIEWS ARE FOR PRESENTATION ONLY, CONSTRUCTION DOCUMENTS TAKE PRECEDENCE.

DRAWING INDEX:		PROJECT INFO:	CODE COMPLIANCE:
C1	COVER SHEET	TWO-STORY SINGLE FAMILY RESIDENCE	INTERNATIONAL RESIDENTIAL CODE (IRC) 2012 INTERNATIONAL ENERGY CONSERVATION CODE (IECC) 2015 TYPE OF CONSTRUCTION: GROUP R-3 RESIDENTIAL SINGLE FAMILY DWELLING, WOOD FRAME
S1	SITE PLACEMENT		
1	FIRST FLOOR PLAN		
2	SECOND FLOOR PLAN		
3	ELEVATIONS		
4	ELEVATIONS		
5	CROSS SECTIONS		
6	ROOF PLAN		
7	SLAB LAYOUT	REVISION HISTORY:	
8	FIRST FLOOR W/ FUTURE GARAGE		DATE: COMMENTS:
M1	MILLWORK		
E1	FIRST FLOOR ELECTRICAL PLAN		
E2	SECOND FLOOR ELECTRICAL PLAN		

Great care and effort have gone into the creation of these plans, however, because of the impossibility of providing on-site supervision and control over actual construction and because of the great variance in local building codes and conditions, DCA Design LLC assumes no responsibility for any damage due to any deficiencies, omissions or errors in these plans.

These drawings are to be considered a "builder's set" of plans and are merely a guide to indicate design intent. The builder is responsible for providing good building practices and knowledge to result in a sound, code compliant and weatherproof home. DCA Design LLC assumes no liability for any home which may be built from these plans.



David Cox, cpbd


Houston, TX
832.604.6686 office
dcox@designdca.com
www.designdca.com



GARCIA/CABALLERO RESIDENCE

REVISIONS	
DATE	ITEM
JOB NUMBER 18-054	
DATE	06-12-19
SCALE AS NOTED	
DRAWN	DC

C1

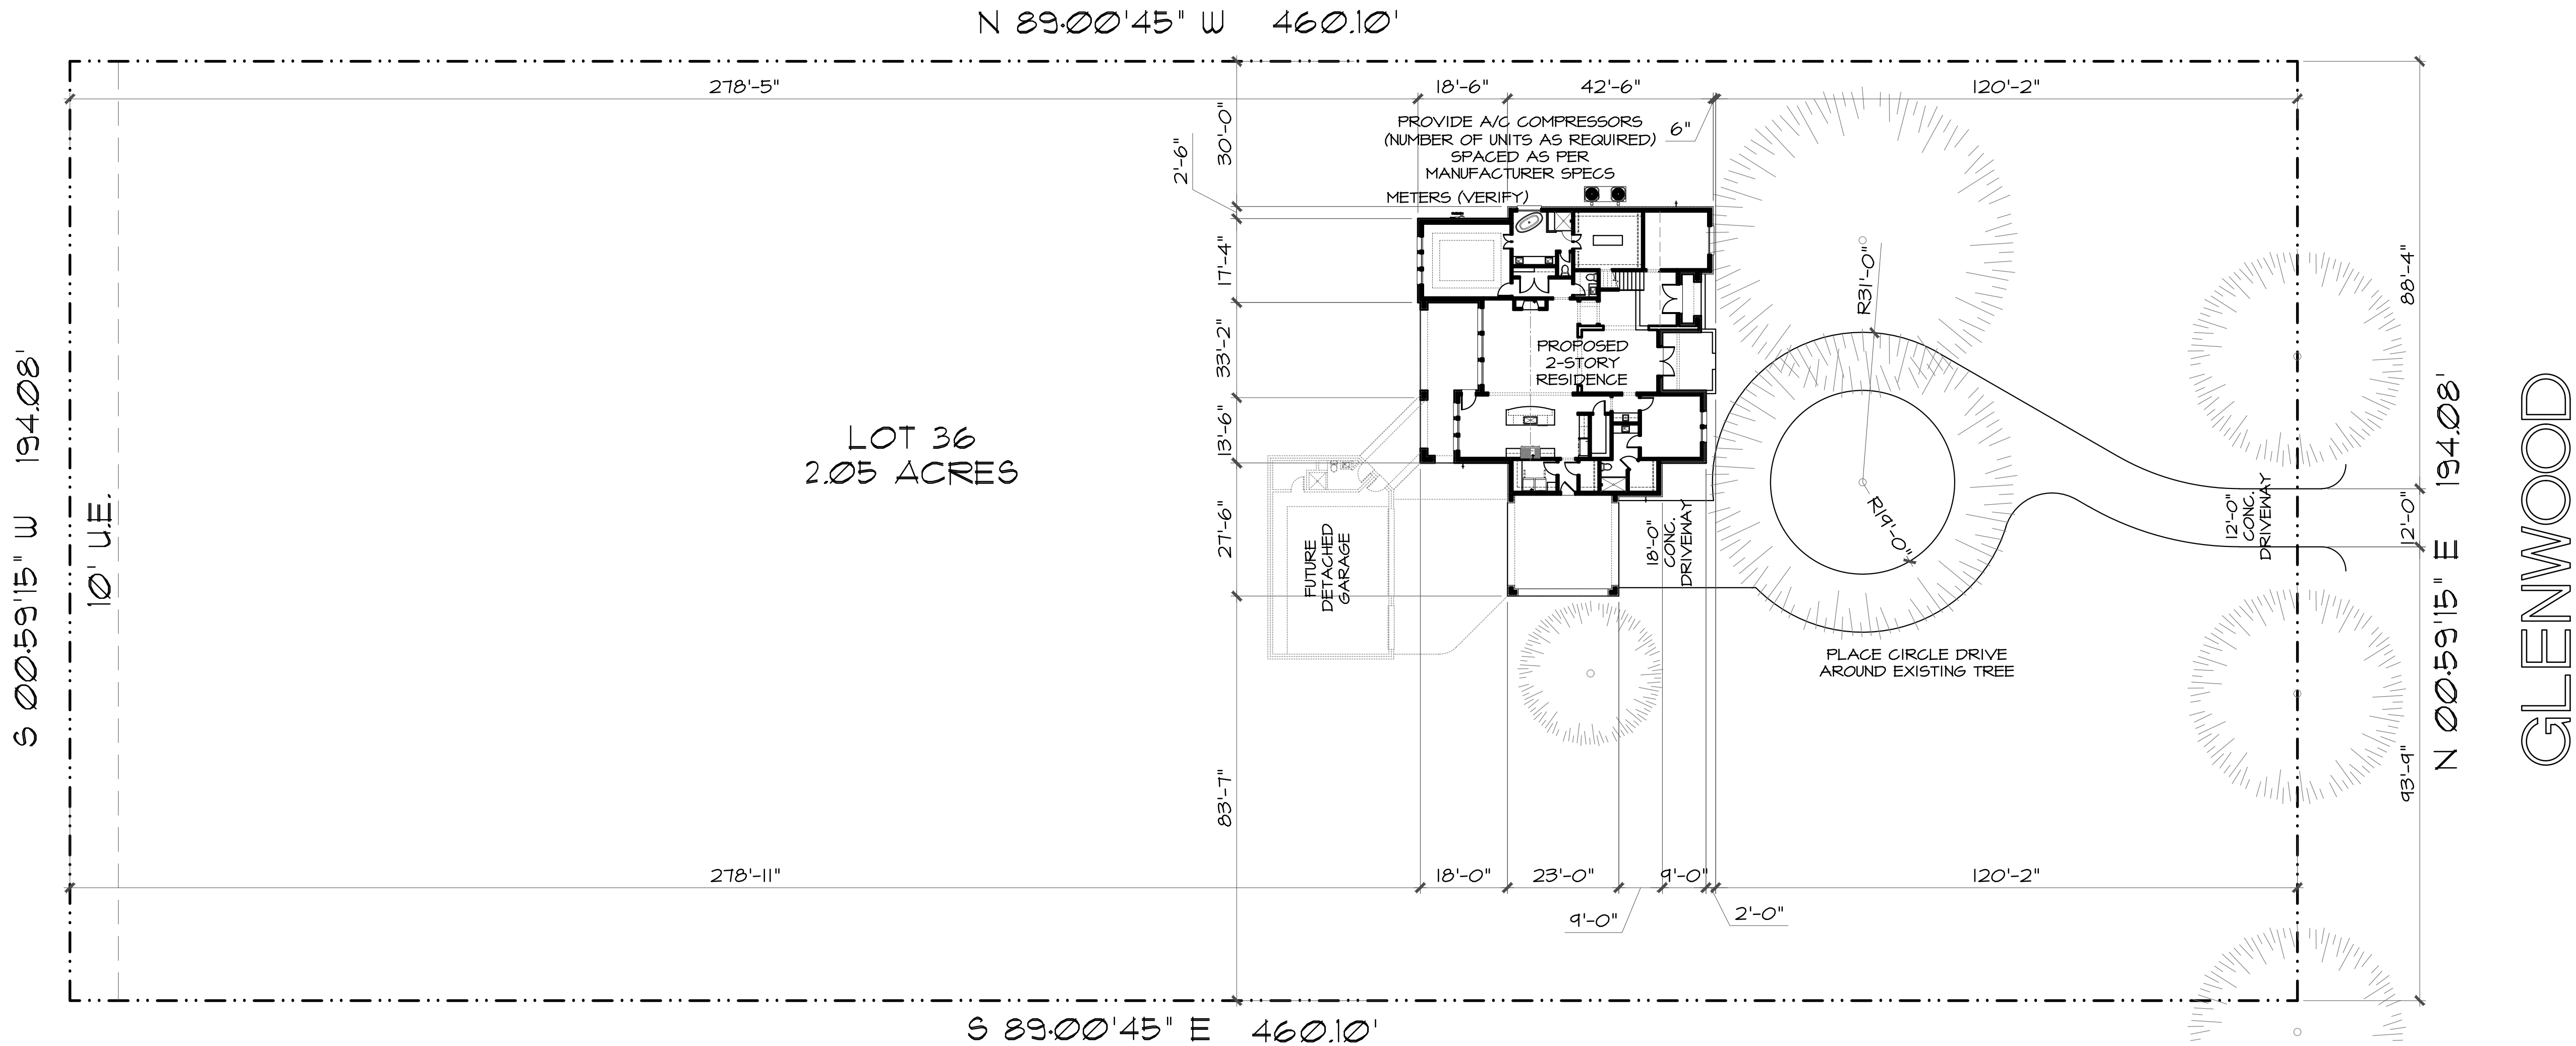


1 SITE PLAN

1" = 20'-0"


1. FINISHED FLOOR ELEVATIONS SHALL BE A MINIMUM OF 12' ABOVE THE TOP OF THE NEAREST SANITARY SEWER MANHOLE COVER OR CROWN OF STREET.
2. BUILDER TO VERIFY PLACEMENT OF HOME ON LOT AND LOCATION OF ALL EASEMENTS AND BUILDING LINES PRIOR TO CONSTRUCTION.
3. PLUMBER TO VERIFY THE LOCATION OF WATER METERS AND TO CONTACT LOCAL AUTHORITY TO CONNECT. WATER PIPE AND METER SIZES TO CONFORM WITH 2000 U.P.C. PIPING TO BE SCHEDULE 40 PVC OR EQUAL.
4. ALL DRAINAGE AND RUN-OFF SHALL BE DIRECTED TO THE STREET. DRAINAGE AND RUN-OFF IS NOT ALLOWED TO BE DIRECTED ONTO ADJACENT PROPERTIES.

SEPTIC SYSTEM & FIELD
DESIGN BY OTHERS

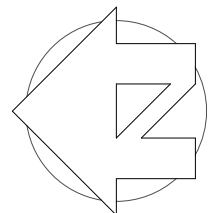

David Cox, cpbd

Houston, TX
832.604.6686 office
dcox@designdca.com
www.designdca.com

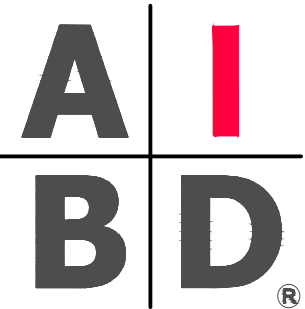

GARCIA/CABALLERO RESIDENCE

REVISIONS


DATE	ITEM


JOB NUMBER 18-054

DATE 06-12-19


SCALE AS NOTED

DRAWN DC

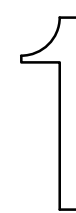

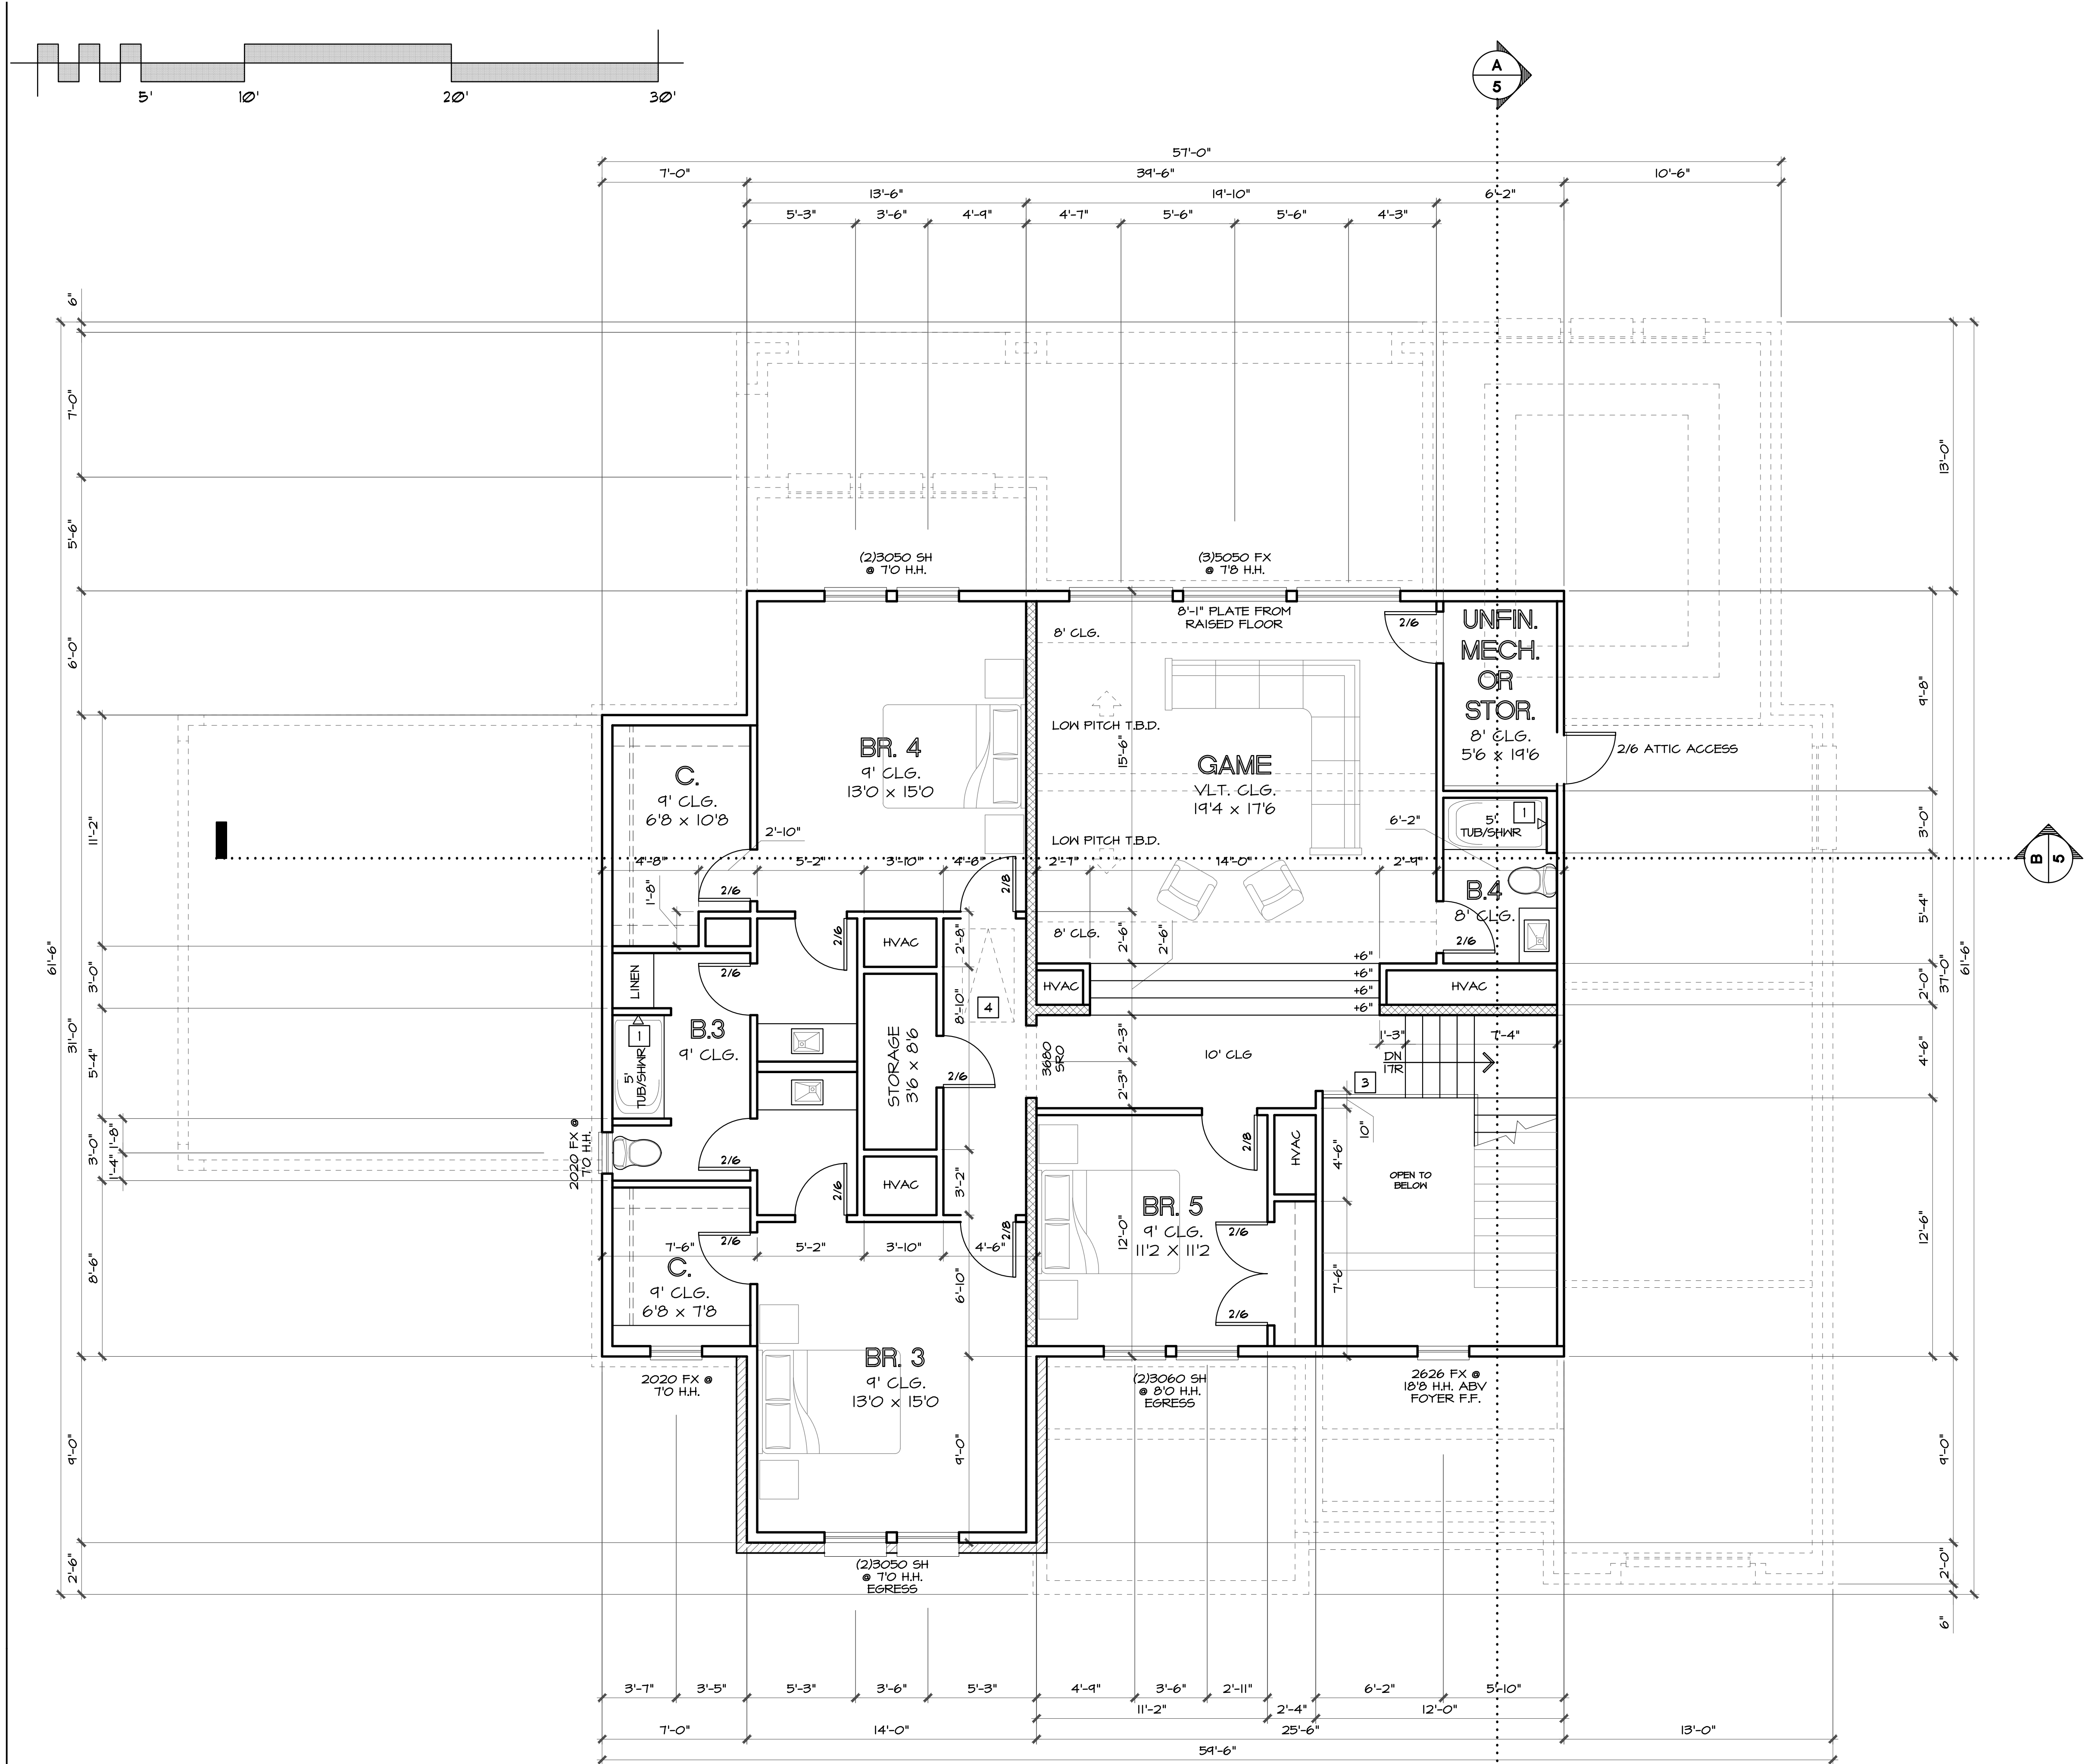

INTERIOR ELEVATION
VIEW INDICATOR

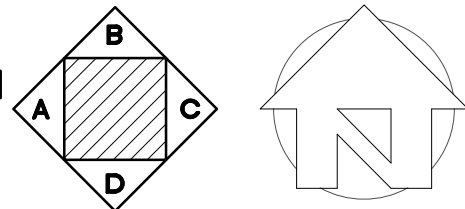

1 2ND FLOOR PLAN

1/4" = 1'-0"
8'-0" HIGH DOORS U.N.O.
8'-0" HEADER HGT. U.N.O.
2x6 EXTERIOR WALLS U.N.O.
2x4 INTERIOR WALLS U.N.O.
[Hatched Box] = 2x6 INTERIOR WALL

WINDOW CALL-OUT EXPLANATION:
WINDOW SIZES GIVEN ARE GENERIC AND DO NOT RELATE TO A PARTICULAR MANUFACTURER
3060 XX ← SH = SINGLE HUNG
FX = FIXED
CSMT = CASEMENT
SLD = SLIDER
6'-0" TALL
3'-0" WIDE
WINDOW MATERIAL (I.e. WOOD, VINYL, ALUMN) IF NOT SPECIFIED IN PLANS IS TO BE DETERMINED BY BUILDER'S SPECIFICATIONS

NOTE: GUARDRAILS SHALL BE IN COMPLIANCE WITH SECTION R312. BALUSTERS SHALL NOT BE SPACED WHERE A SPHERE OF 4" CANNOT PASS THROUGH.
NOTE: HANDRAILS AND GUARDRAILS SHALL COMPLY WITH THE MINIMUM UNIFORMLY DISTRIBUTED LIVE LOADS AS PER TABLE R301.5
NOTE: ALL FIREPLACES SHALL COMPLY WITH SECTION R1001 (MASONRY) OR R1004 (FACTORY-BUILT). TERMINATE CHIMNEY 2'-0" ABOVE ANY SURFACE WITHIN 10'-0".
NOTE: ATTIC STAIR SHALL COMPLY WITH SECTION M1305.1.3 AS AMENDED BY THE CITY OF HOUSTON (CLEAR OPENING MIN. 30" x 54", MIN. 350 LB. CAPACITY)
NOTE: PROVIDE TEMPERED GLAZING PER SECTION R308.4

PLAN KEYNOTES:
SEE SHEET I




David Cox, cpbd

Houston, TX
832.604.6686 office
dcox@designdca.com
www.designdca.com




GARCIA/CABALLERO RESIDENCE


REVISIONS	
DATE	ITEM
JOB NUMBER 18-054	
DATE	06-12-19
SCALE	AS NOTED
DRAWN	DC

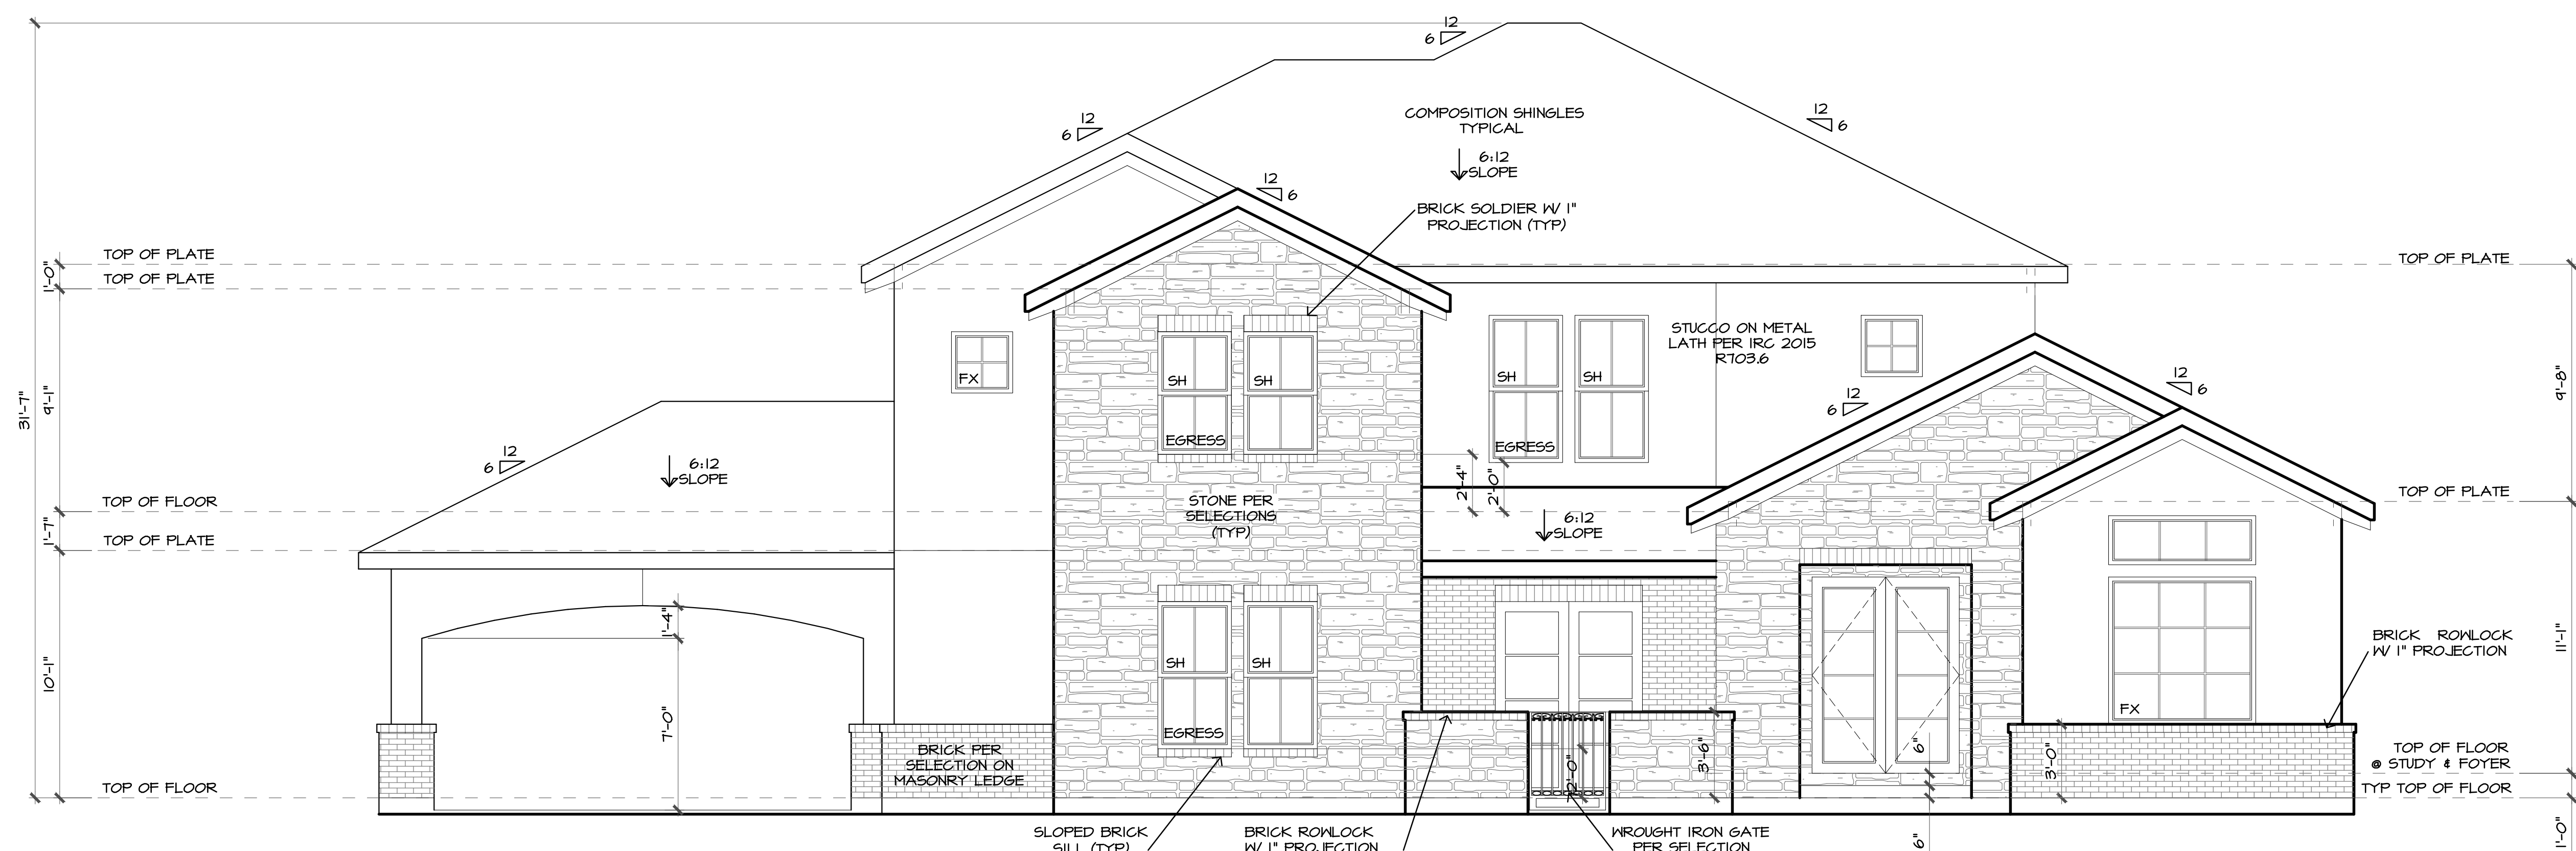

1) $1/4'' = 1'-0''$

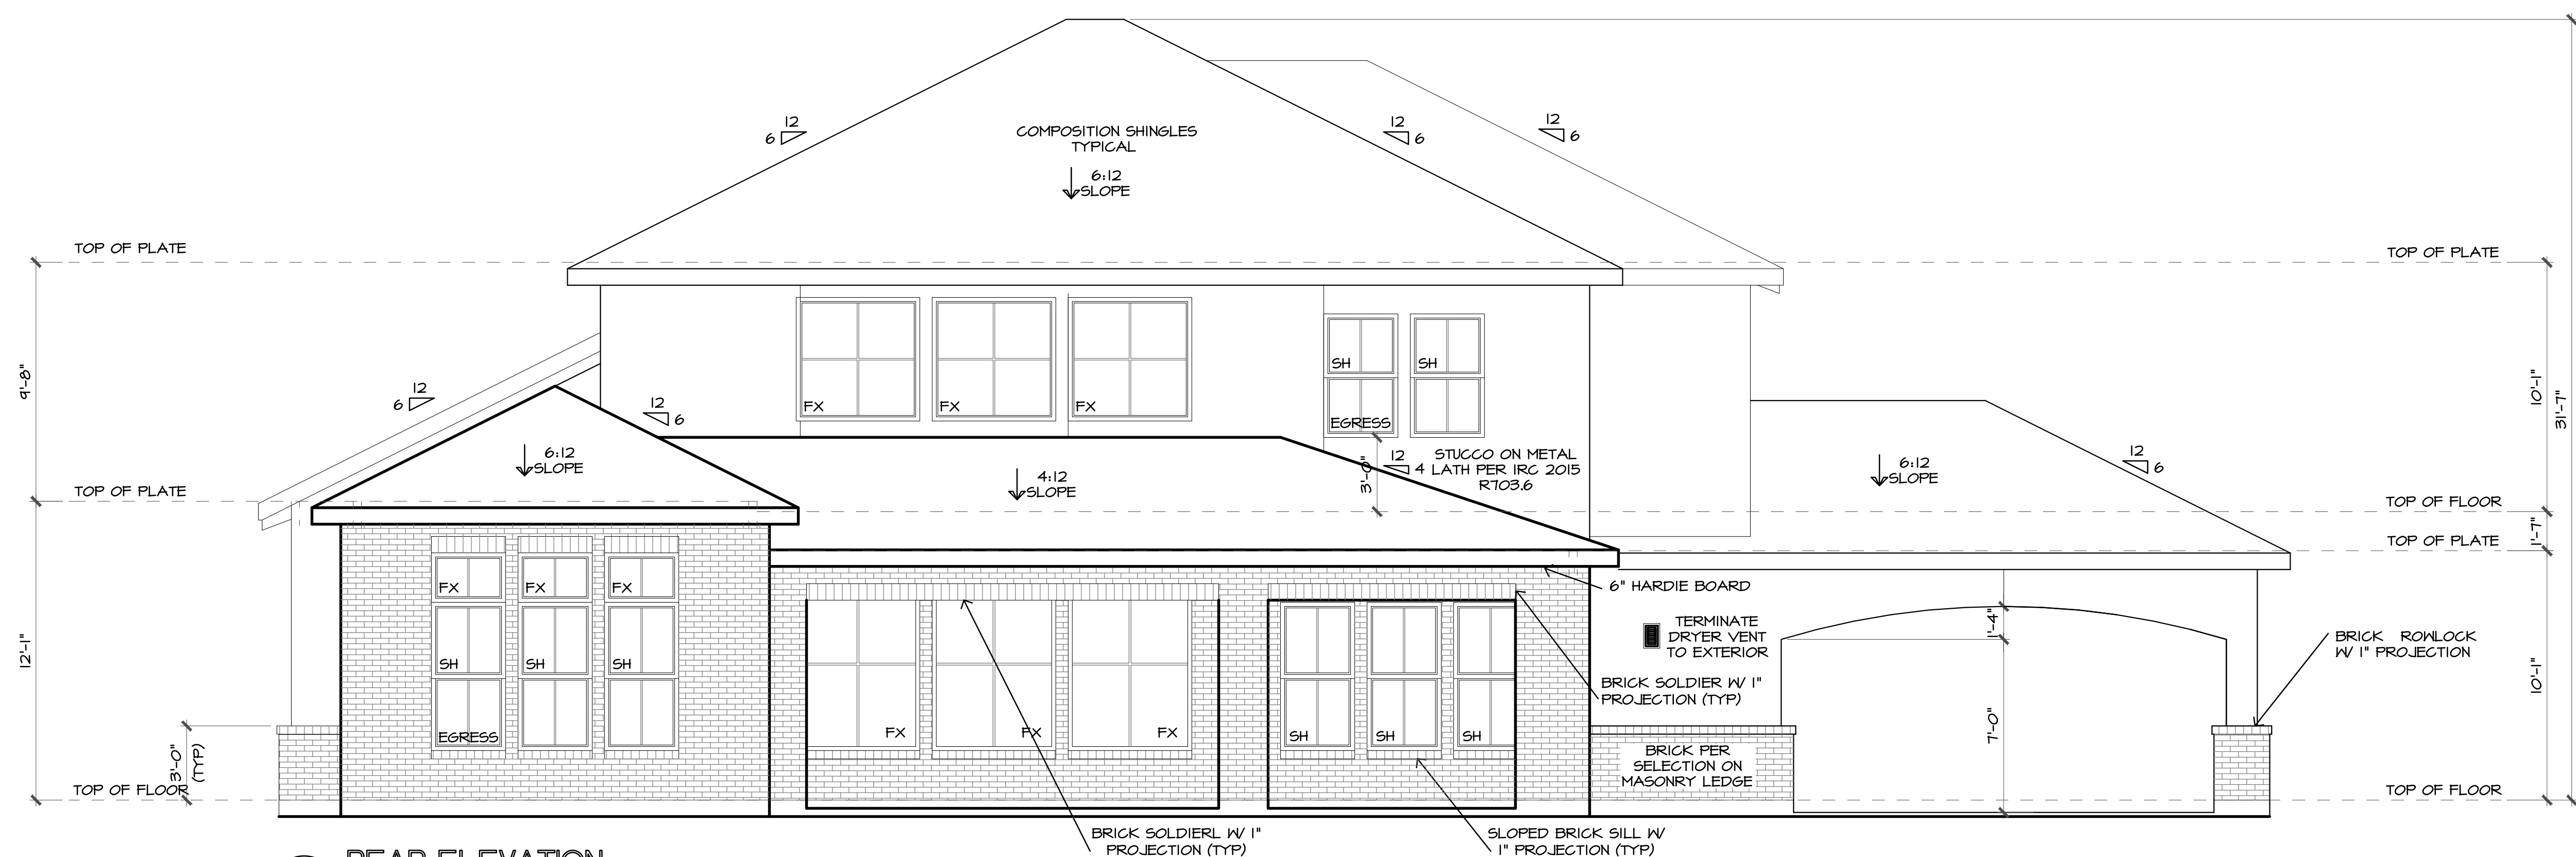


2) $\frac{1}{4}'' = 1'-0''$

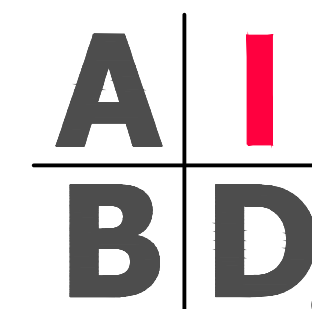

GARCIA/CABALLERO RESIDENCE

REVISIONS	
DATE	ITEM
JOB NUMBER 18-054	
DATE	06-12-19
SCALE	AS NOTED
DRAWN	DC

3

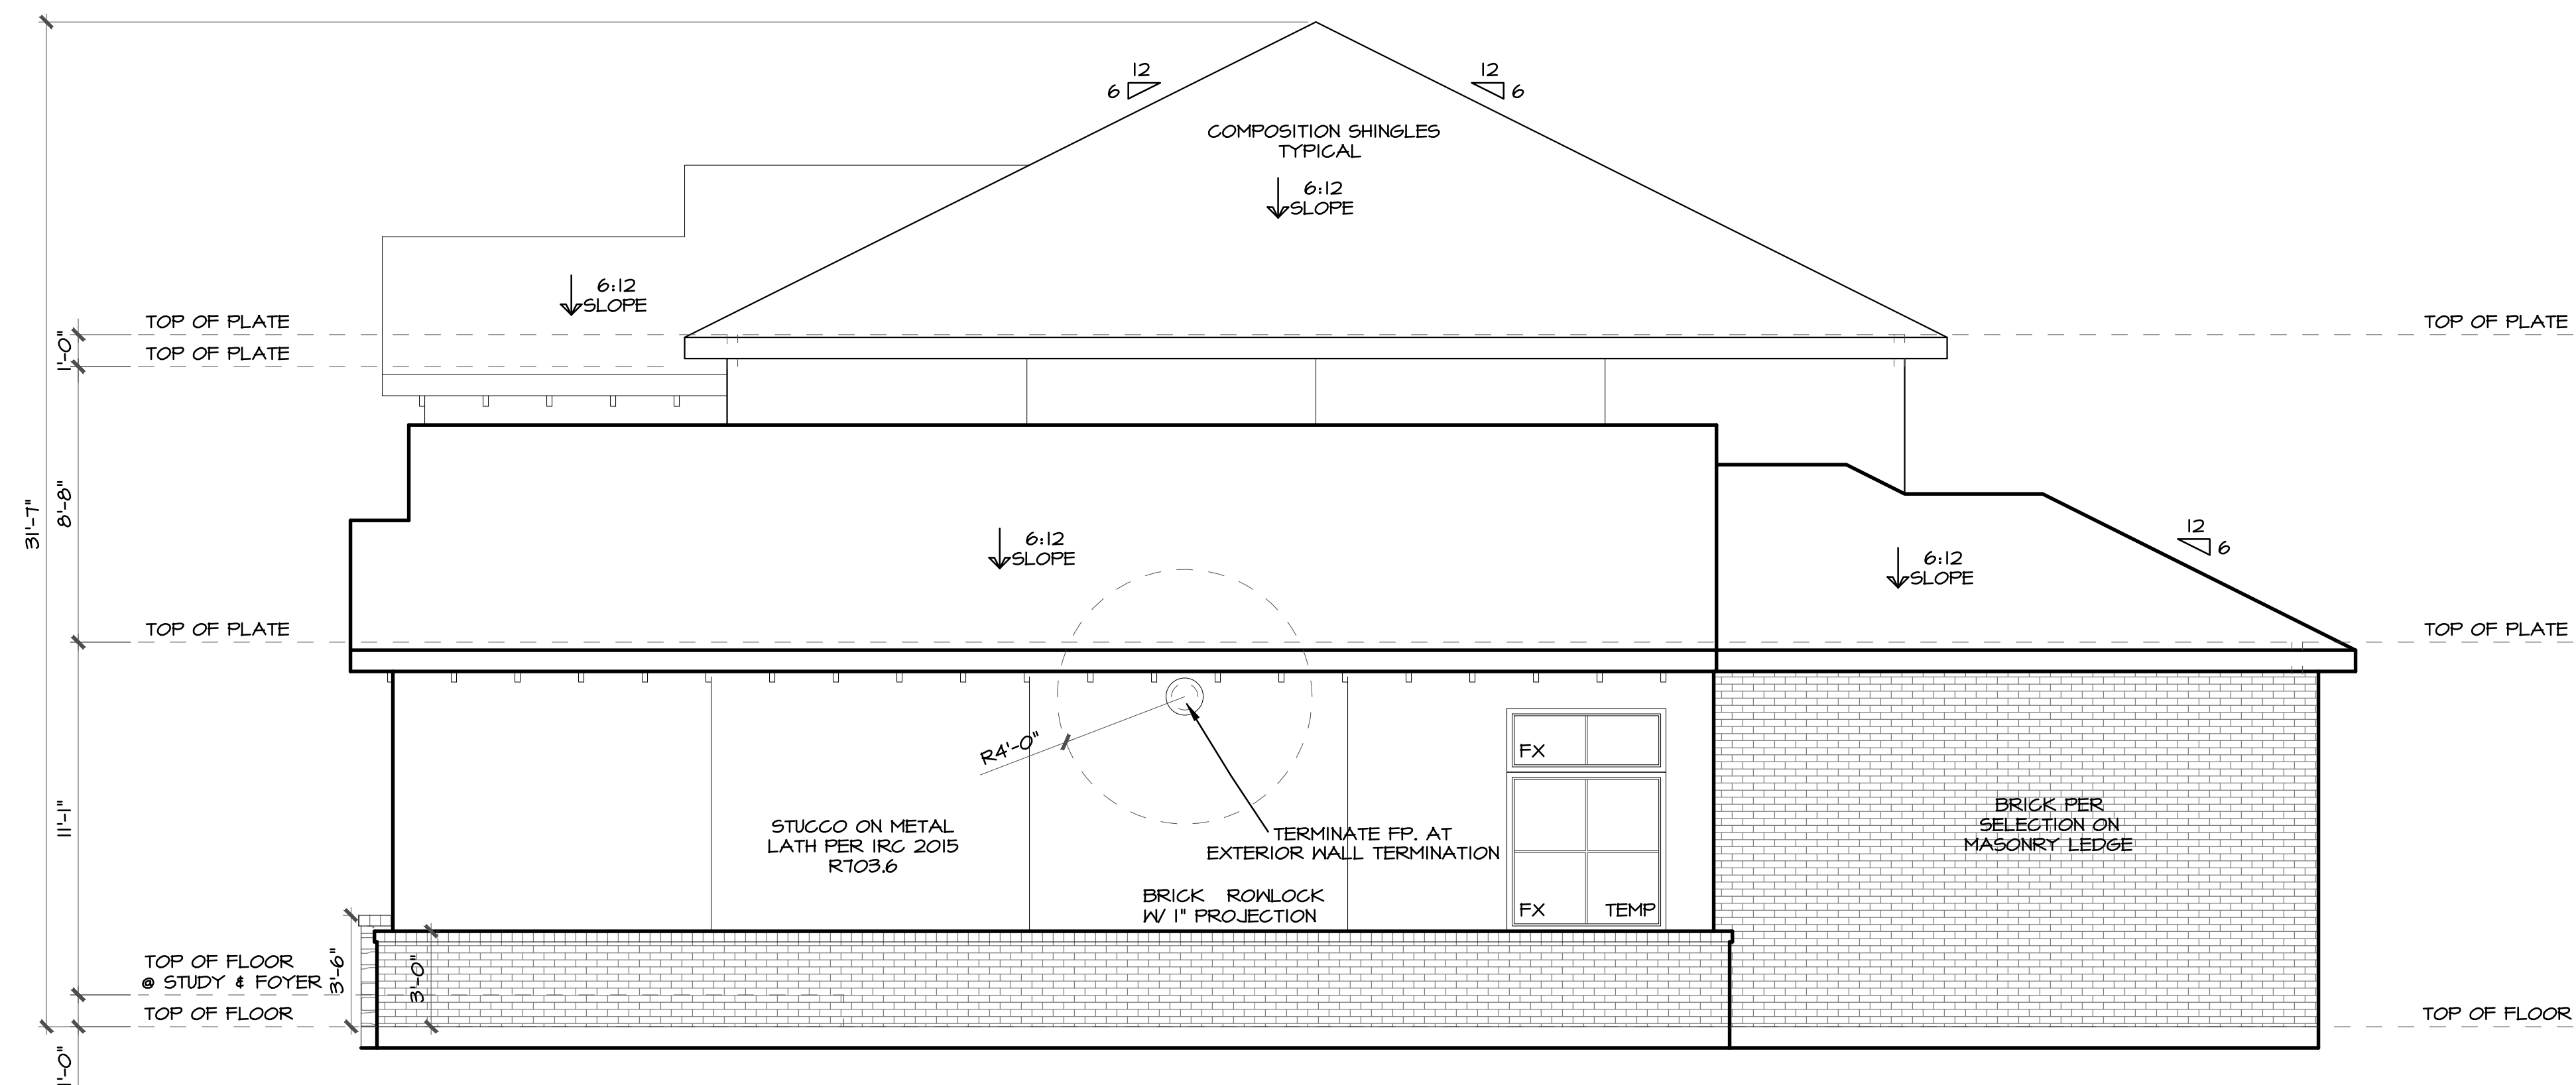


Architectural elevation drawing of a building facade. The drawing includes the following details:

- Roof Pitches:** Multiple roof sections are shown with pitches of 6:12 and 4:12, indicated by slope triangles.
- Materials:**
 - Composition shingles typical on the main roof.
 - Stucco on metal lath per IRC 2015 R703.6 on the main wall.
 - Stone per selections (TYP) on the right side of the facade.
 - Brick per selection on masonry ledge.
 - Brick Ronlock w/ 1" projection on the base.
- Structural and Detail Callouts:**
 - 6" Hardie Board on the lower left roof edge.
 - 6" x 6" window opening with a cross-hatch pattern.
 - Terminate hood vt. at exterior wall termination (pointing to a curved roofline detail).
 - R4'-0" radius callout for a curved masonry element.
 - 3'-0" dimension for a base section.
 - 3'-6" dimension for a base section.
- Level Markers:**
 - TOP OF PLATE (multiple locations)
 - TOP OF GAME ROOM FLOOR
 - TOP OF FLOOR (multiple locations)
 - TOP OF PLATE (multiple locations)
 - TOP OF FLOOR (multiple locations)
- Dimensions:**
 - 1'-0" vertical dimension on the right.
 - 9'-1" vertical dimension on the right.
 - 1'-7" vertical dimension on the right.
 - 10'-1" vertical dimension on the right.


These drawings are to be considered a "builder's set" of plans and are merely a guide to indicate design intent. The builder is responsible for providing good building practices and knowledge to result in a sound, code compliant and weatherproof home. DCA Design LLC assumes no liability for any home which may be built from these plans.





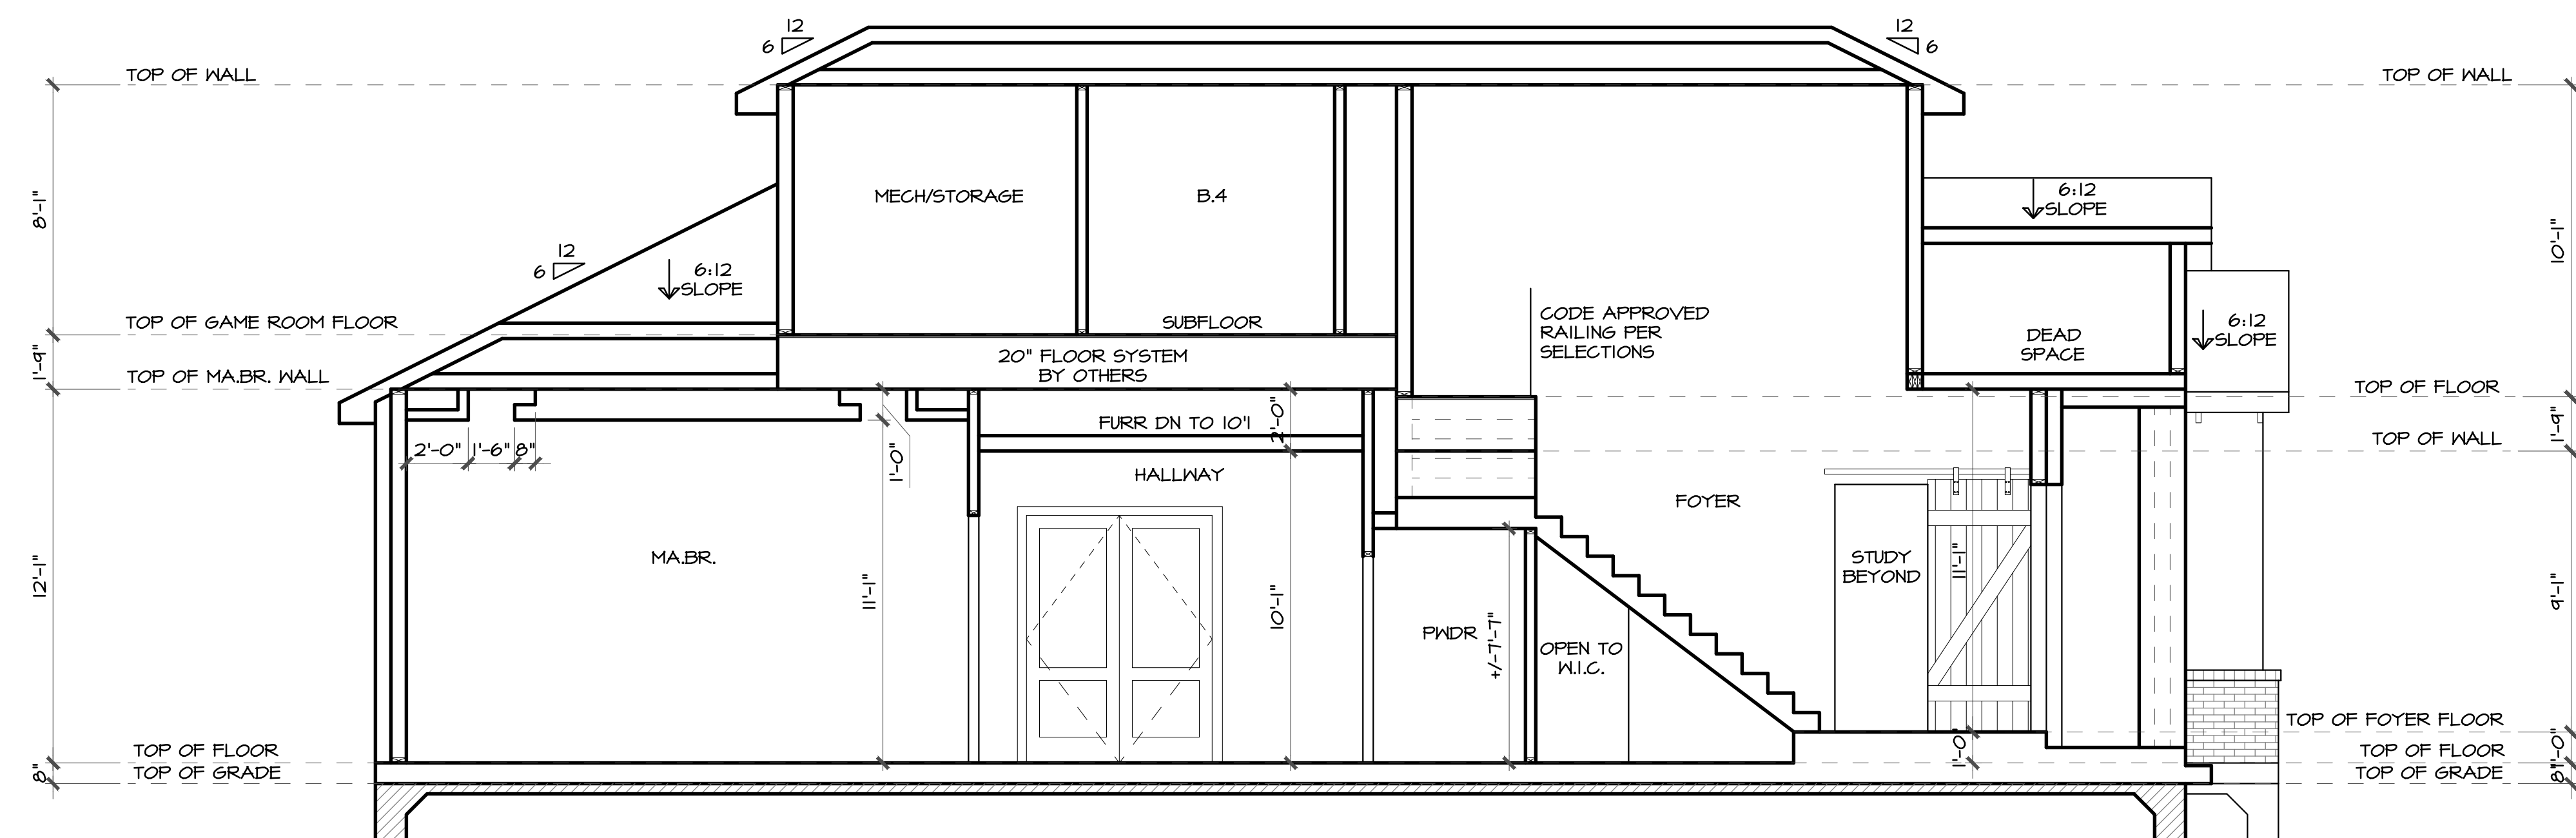



Architectural cross-section drawing of a two-story house. The drawing shows the interior layout with rooms labeled: CLOSET, BR. 4, GAME ROOM, B. 4, LAUN, KITCHEN, FAMILY RM., HALLWAY, and M. BA. Dimensions are provided for various parts: overall height 10'-1", floor height 1'-4", wall height 1'-4", and room heights like 12'-1" for the family room and 11'-1" for the master bedroom. A note at the top center reads: "NOTE: REFER TO ENGINEER'S NOTES FOR SIZE & LOCATION OF FRAMING MEMBERS". The roof is labeled "ATTIC SPACE" and "SLOPE T.B.D.". The drawing also indicates "20" FLOOR SYSTEM BY OTHERS" for both floors.

These drawings are to be considered a "builder's set" of plans and are merely a guide to indicate design intent. The builder is responsible for providing good building practices and knowledge to result in a sound, code compliant and weatherproof home. DCA Design LLC assumes no liability for any home which may be built from these plans.

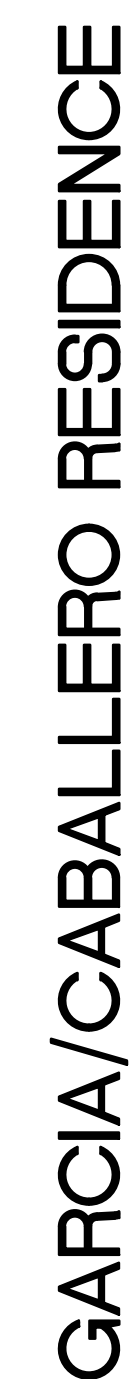

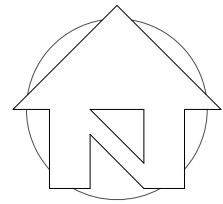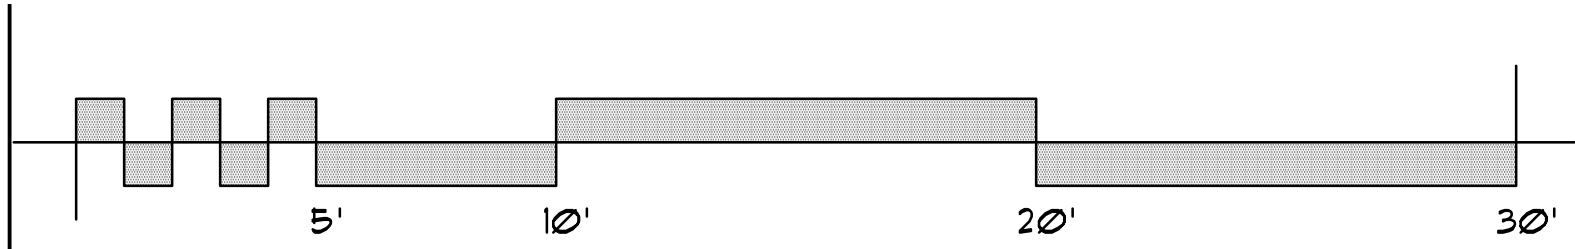


1 ROOF PLAN
1/4" = 1'-0"

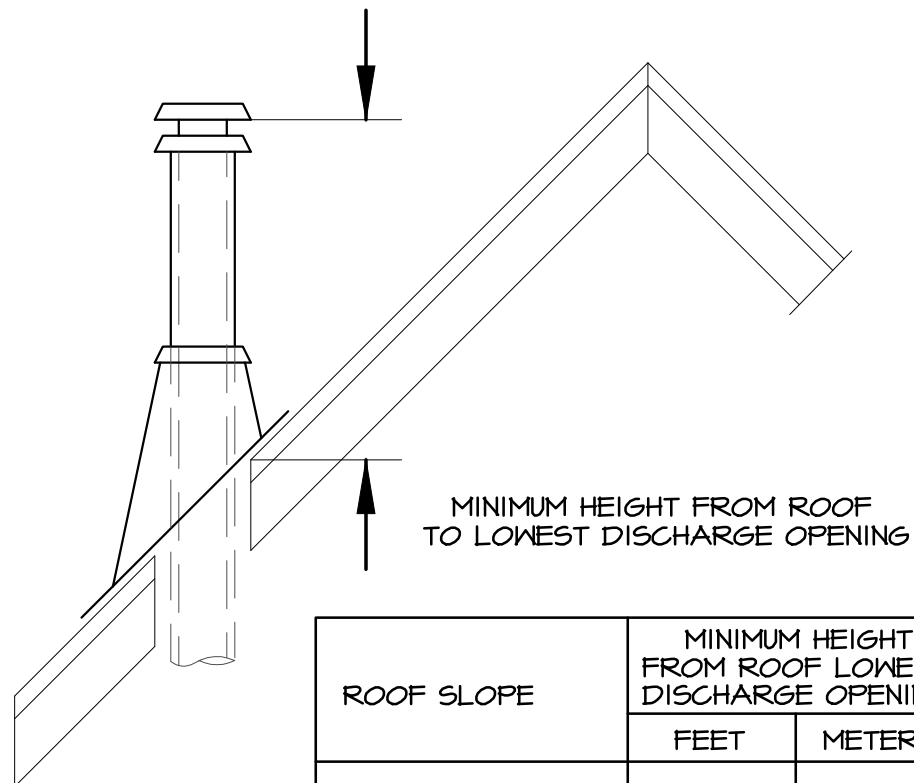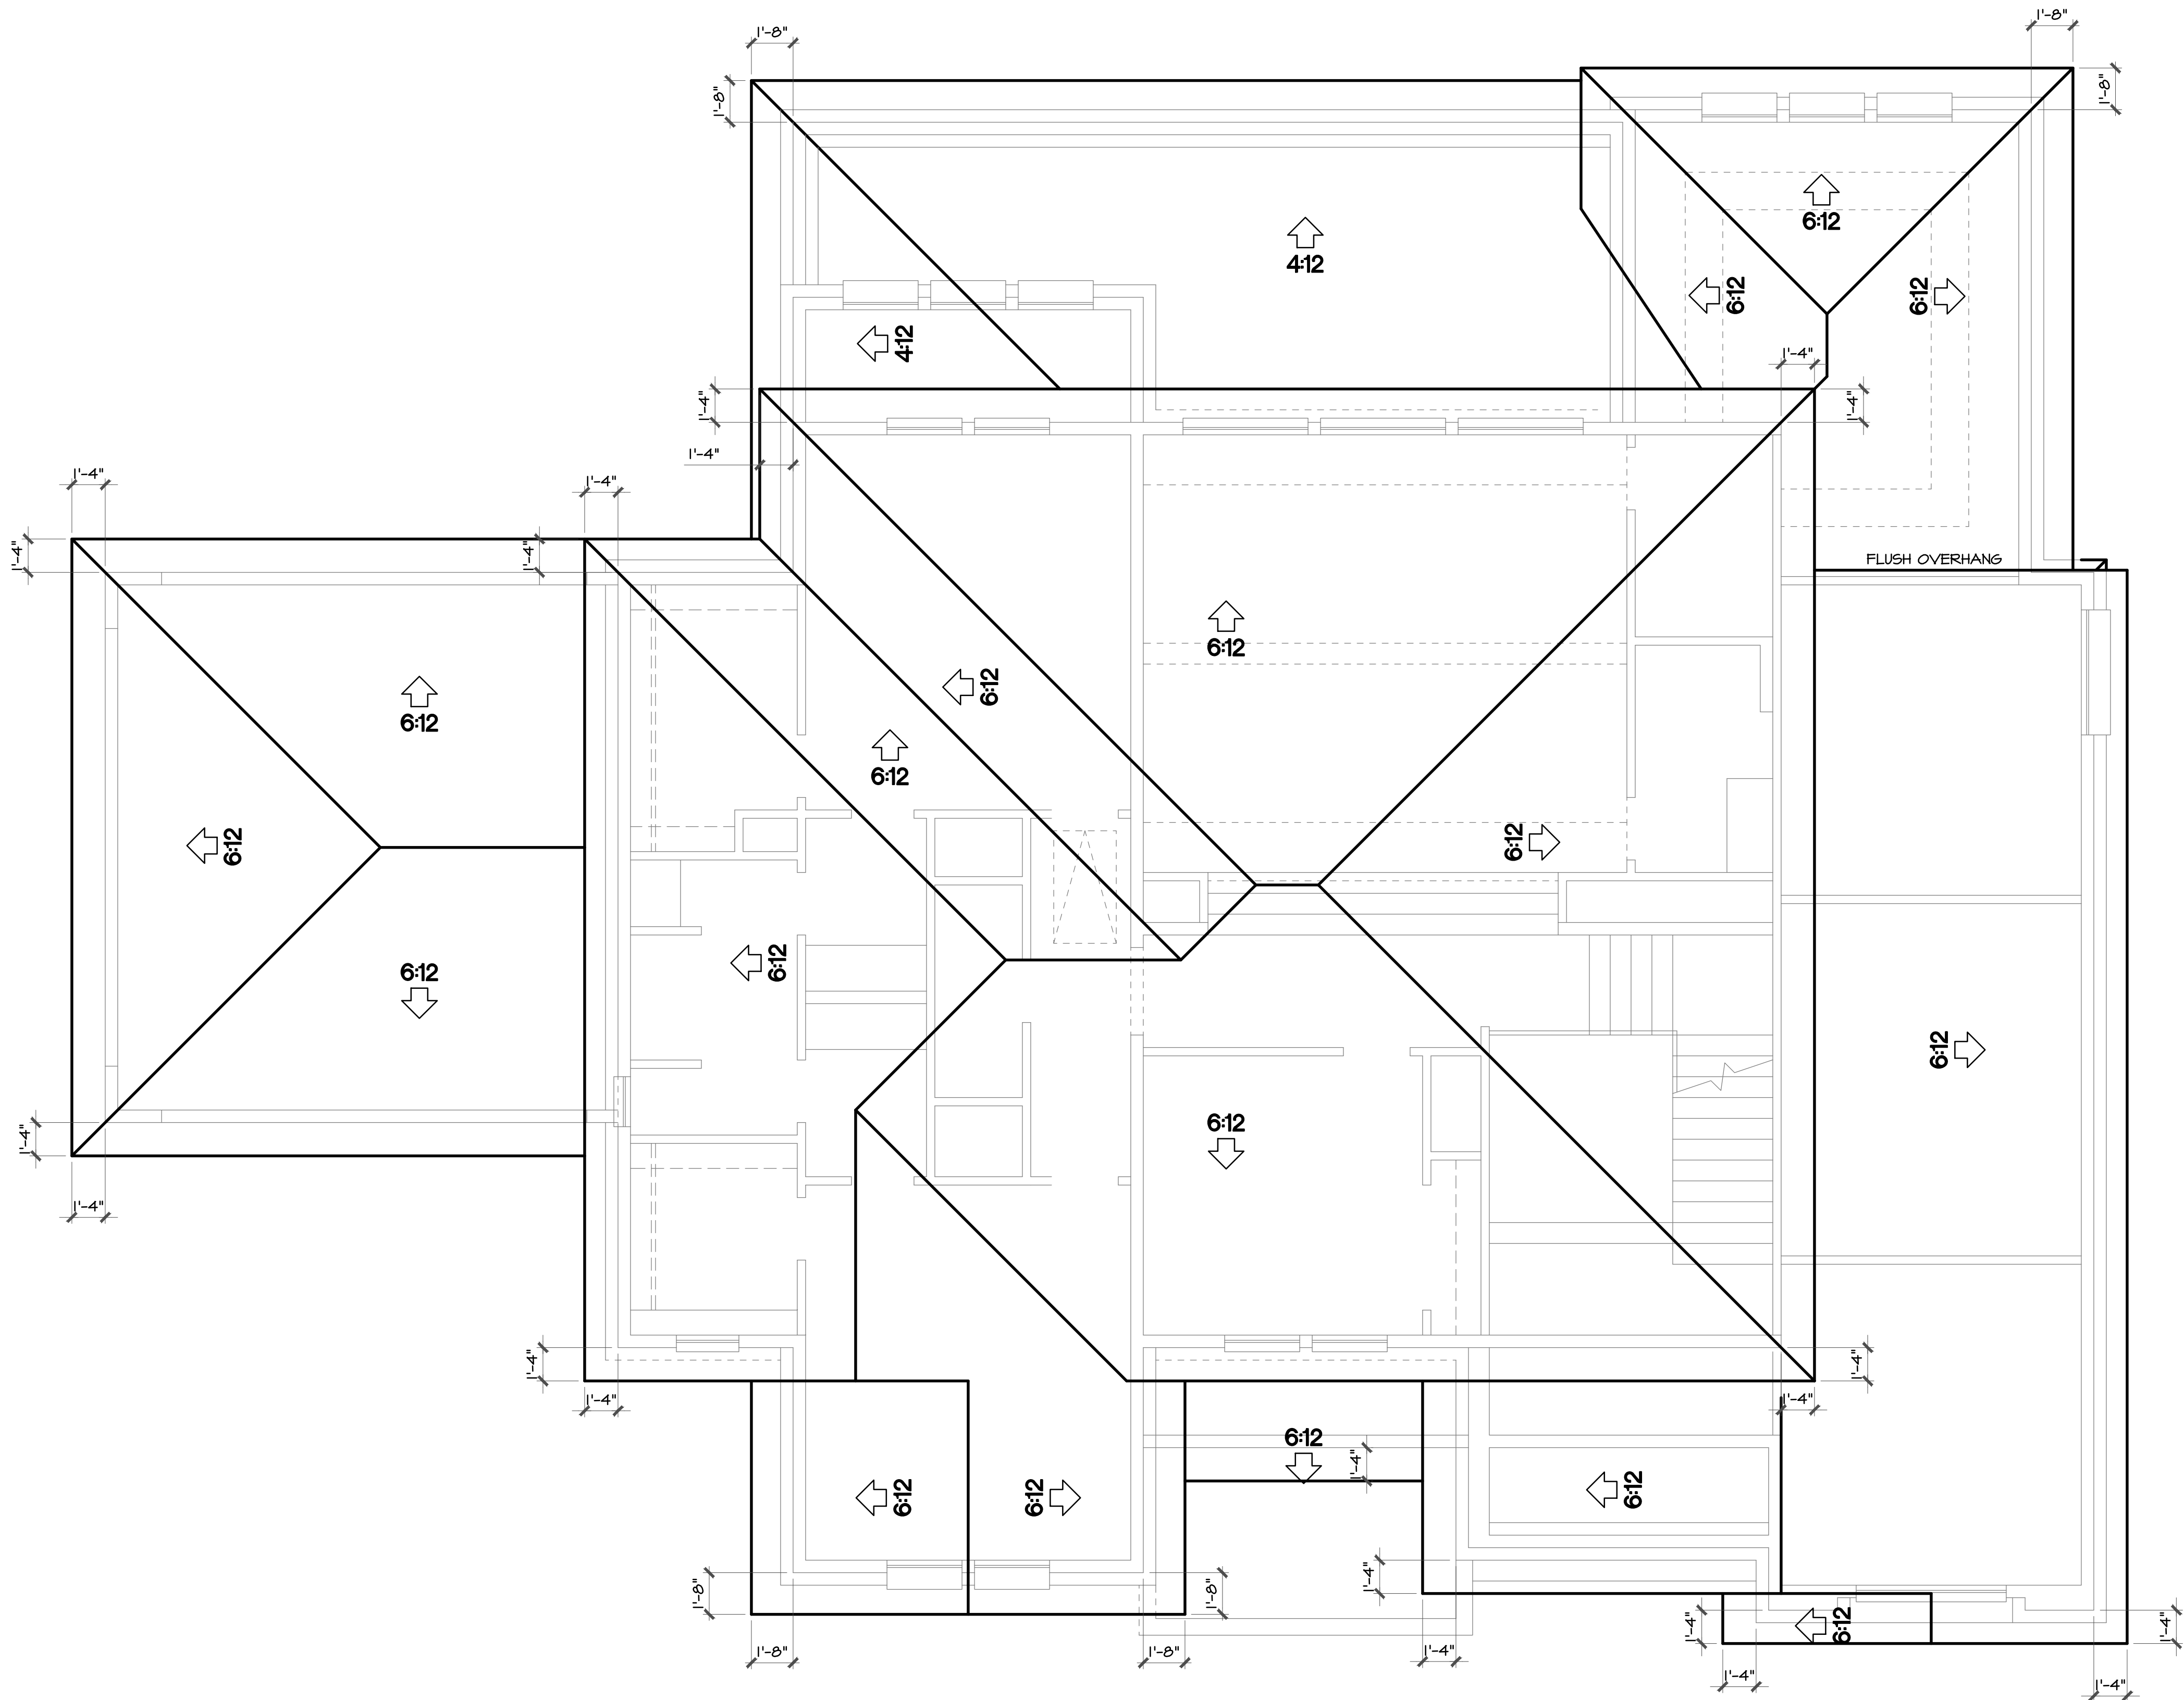

GAS VENT RULE:
GAS VENT CAPS ARE NOT PERMITTED WITHIN 8 FEET (2.4 m) OF A VERTICAL WALL OR SIMILAR OBSTRUCTION


typ. gas venting detail

N.T.S.

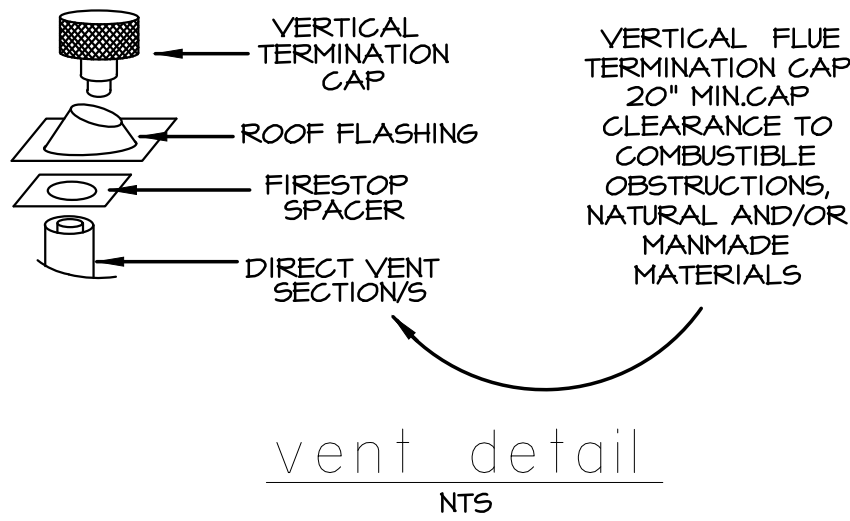

David Cox, cpbd

Houston, TX
832.604.6686 office
dcox@designdca.com
www.designdca.com

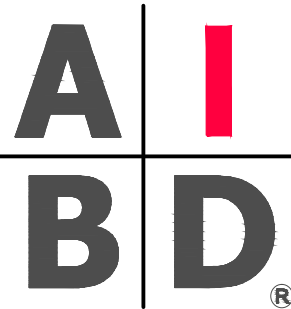

GARCIA/CABALLERO RESIDENCE

REVISIONS

DATE	ITEM

JOB NUMBER 18-054

DATE 06-12-19

SCALE AS NOTED

DRAWN DC




Houston, TX
832.604.6686 office
dcox@designdca.com
www.designdca.com




GARCIA/CABALLERO RESIDENCE

REVISIONS	
DATE	ITEM
JOB NUMBER 18-054	
DATE	06-12-19
SCALE	AS NOTED
DRAWN	DC

7

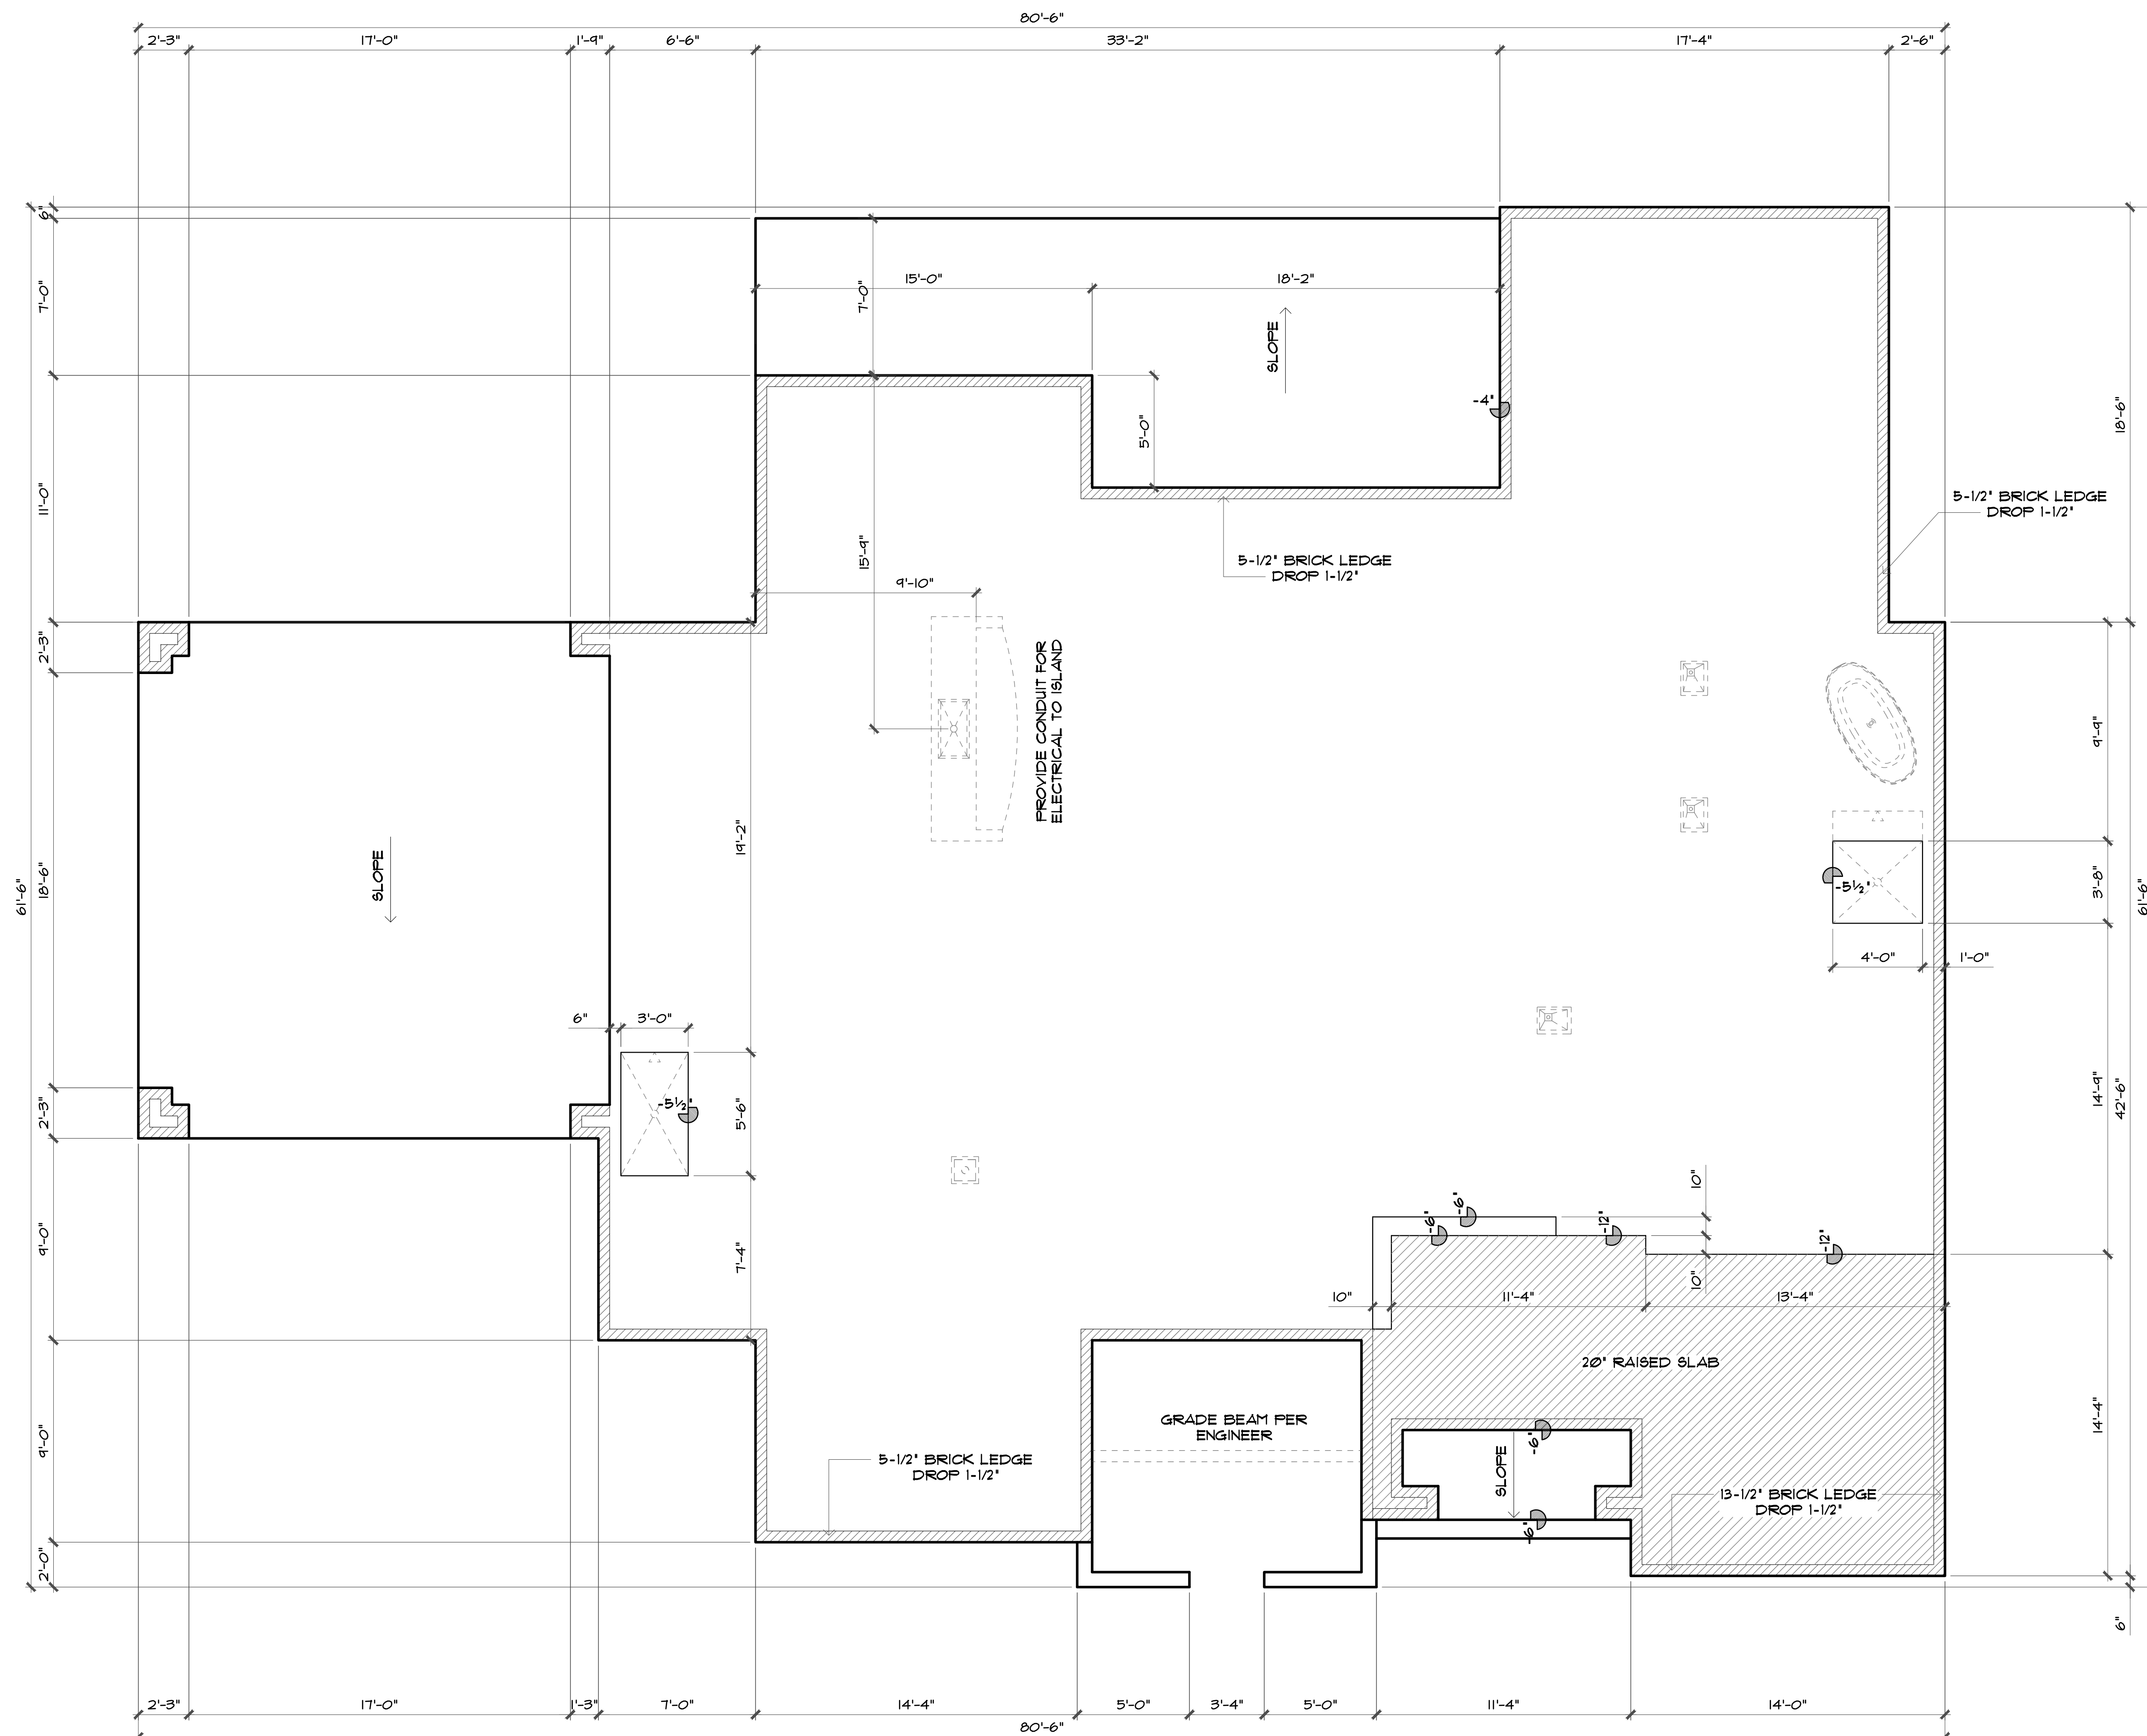
$$1/4'' = 1'-0''$$

NOTE: THIS IS FOR LAYOUT PURPOSES ONLY.
REFER TO ENGINEERING FOR FOUNDATION PLAN
AND DETAILS.

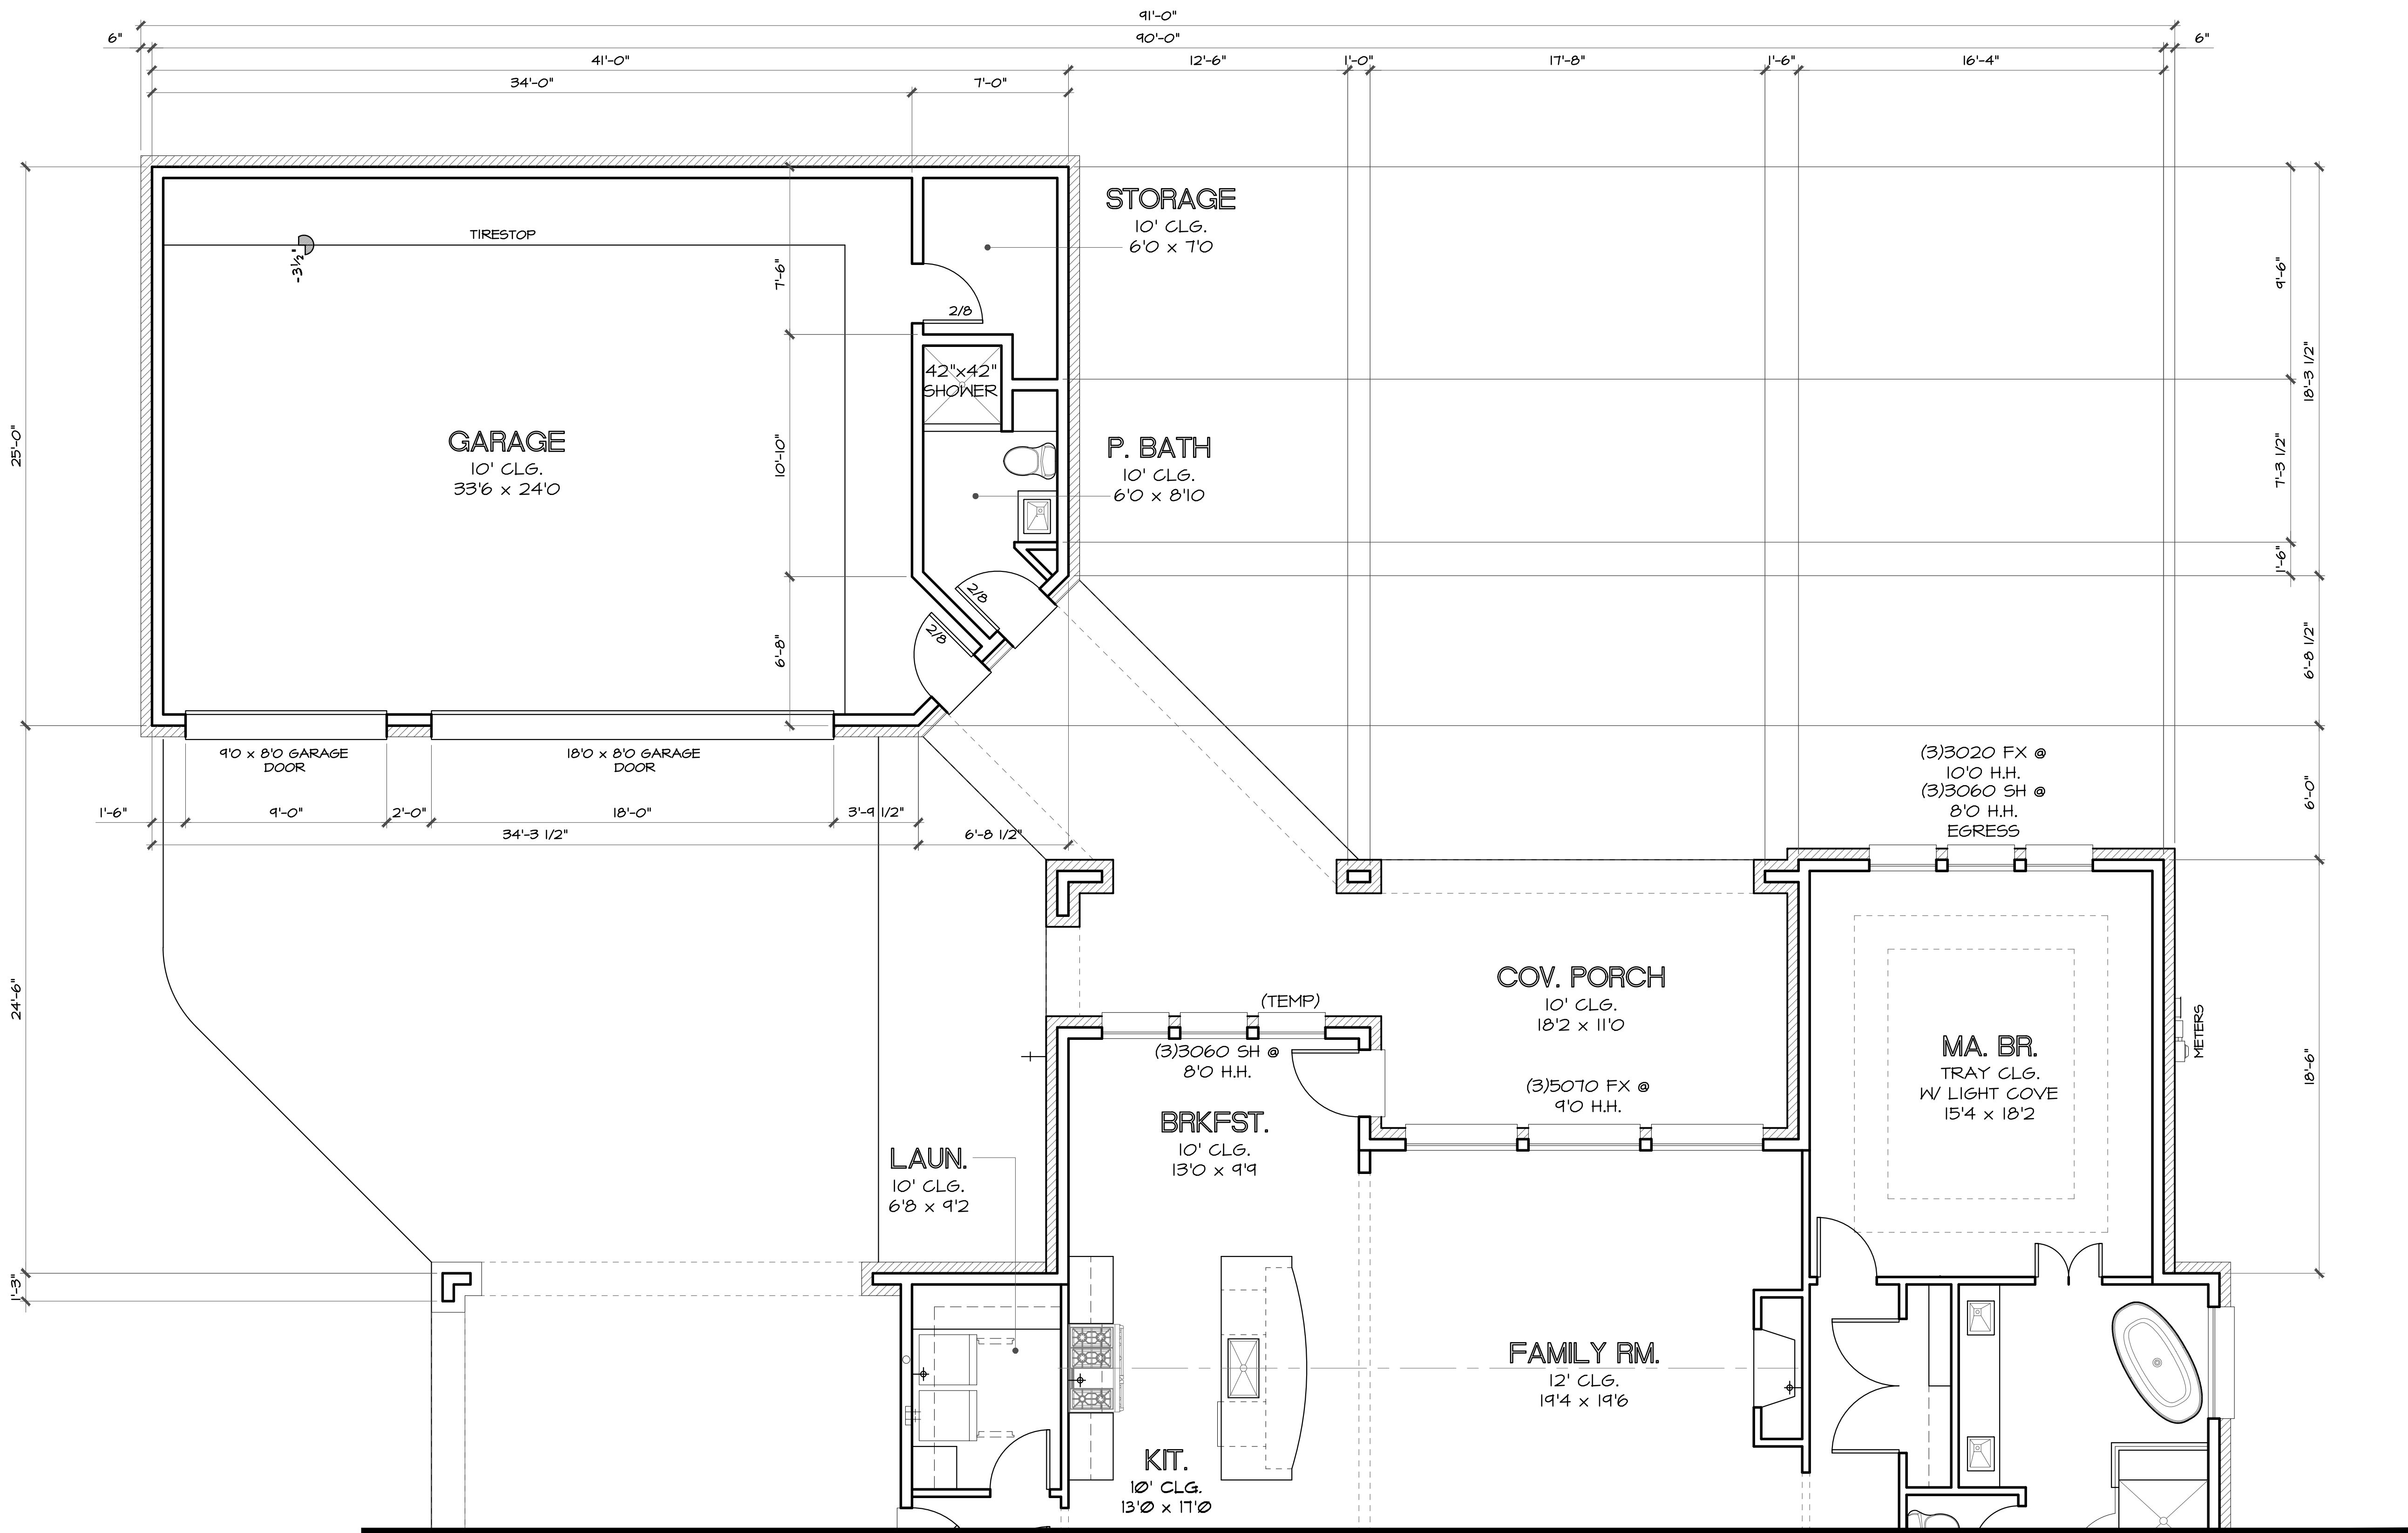

1 1ST FLOOR PLAN W/ FUTURE DETACHED GARAGE
1/4" = 1'-0"

Great care and effort have gone into the creation of these plans, however, because of the impossibility of providing on-site supervision and control over actual construction and because of the great variance in local building codes and conditions, DCA Design LLC assumes no responsibility for any damage due to any deficiencies, omissions or errors in these plans.

These drawings are to be considered a "builder's set" of plans and are merely a guide to indicate design intent. The builder is responsible for providing good building practices and knowledge to result in a sound, code compliant and weatherproof home. DCA Design LLC assumes no liability for any home which may be built from these plans.




David Cox, cpbd

Houston, TX
832.604.6686 office
dcox@designdca.com
www.designdca.com




GARCIA/CABALLERO RESIDENCE


REVISIONS	
DATE	ITEM
JOB NUMBER 18-054	
DATE	06-12-19
SCALE	AS NOTED
DRAWN	DC

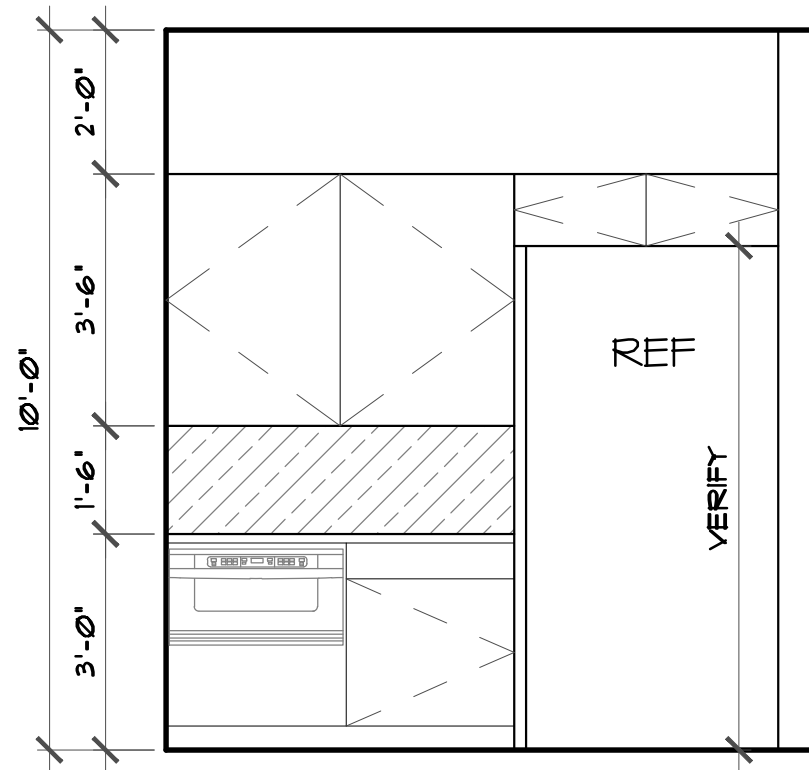


KITCHEN - VIEW D

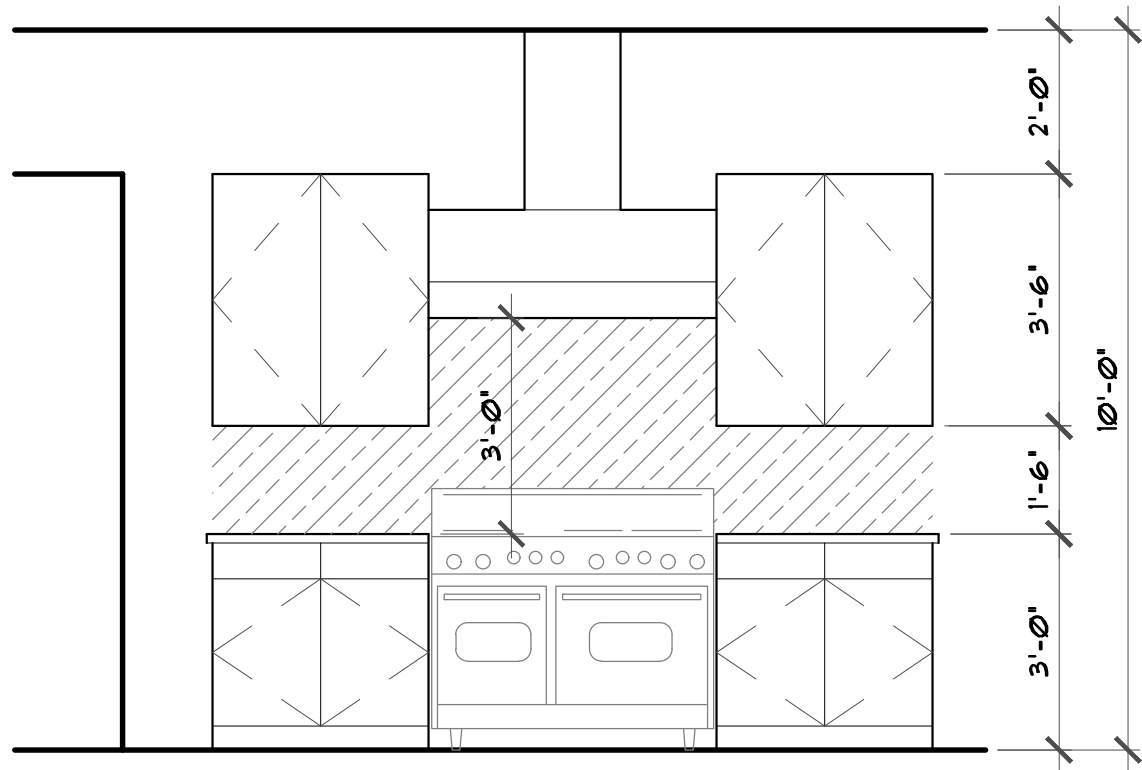


KITCHEN - VIEW A

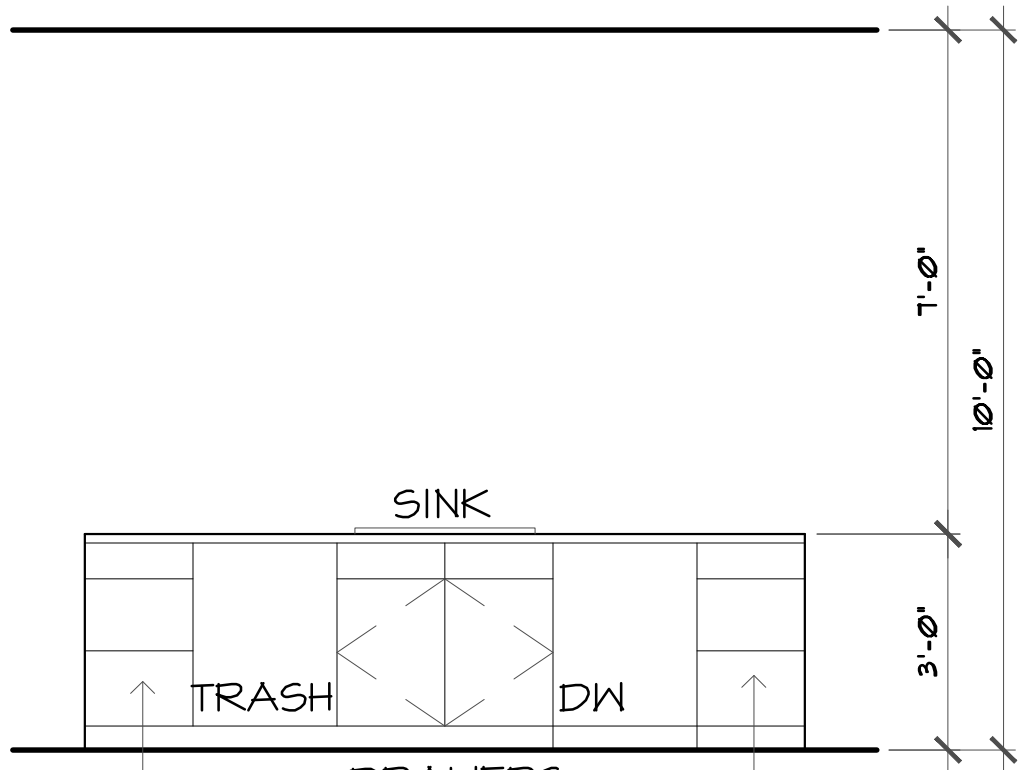


KITCHEN - VIEW C

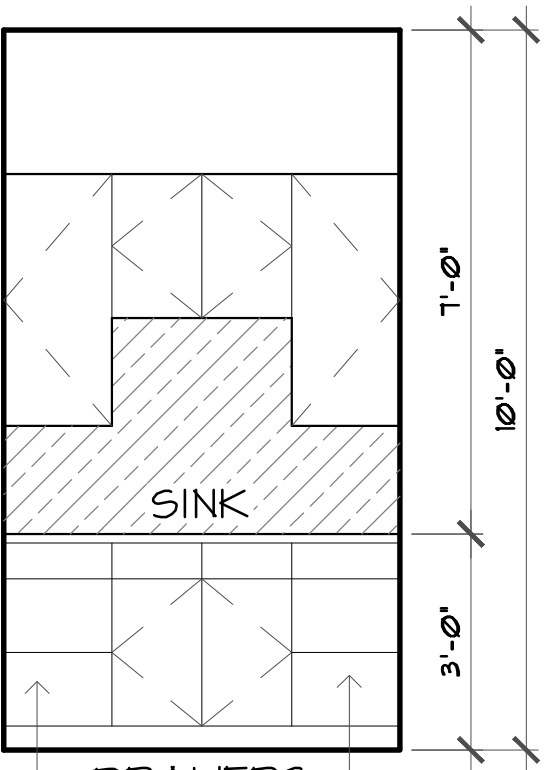


BAR - VIEW A

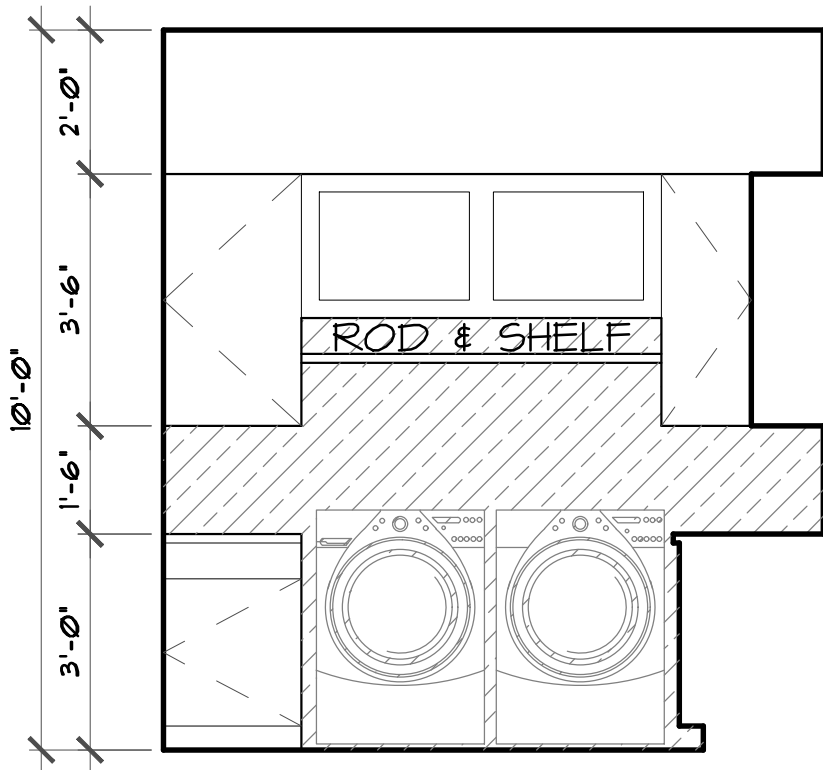


LAUN - VIEW A

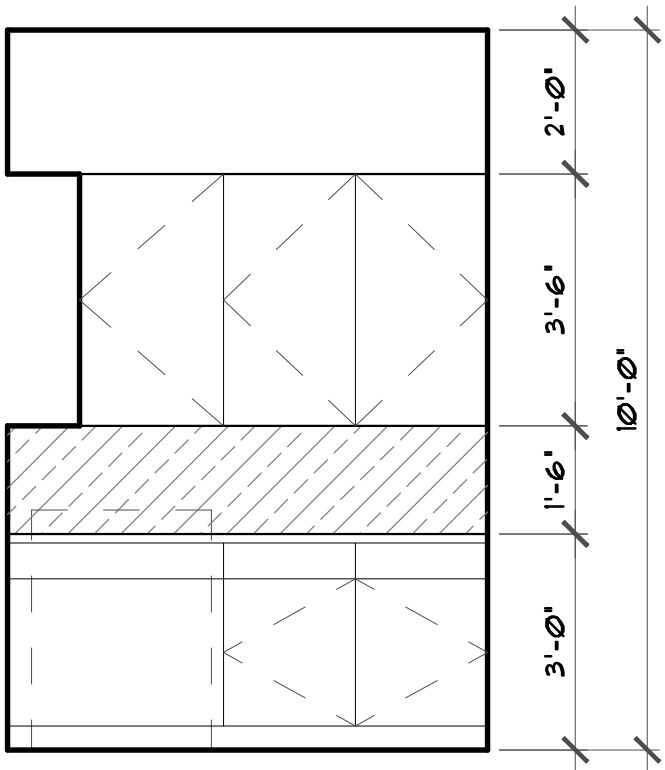


LAUN - VIEW B

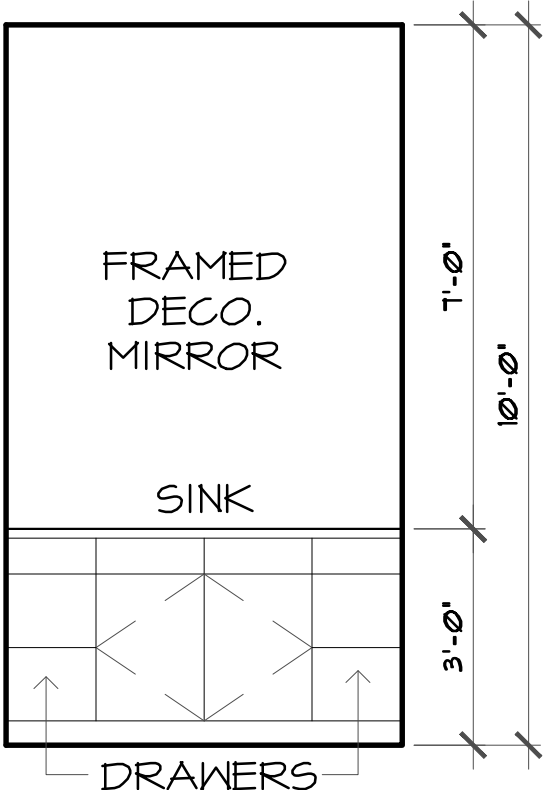


B.2 - VIEW C

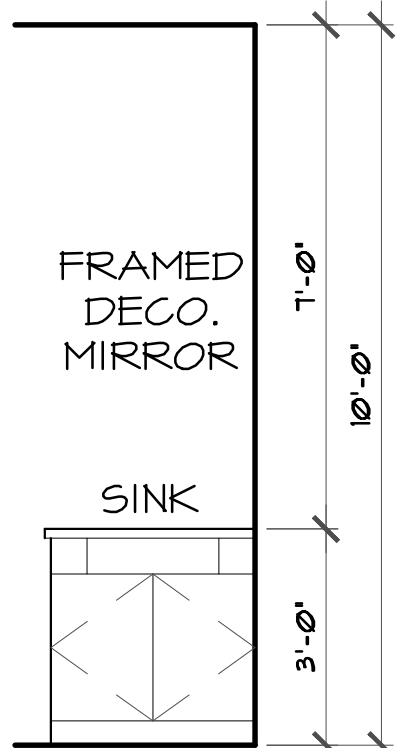


P. - VIEW D

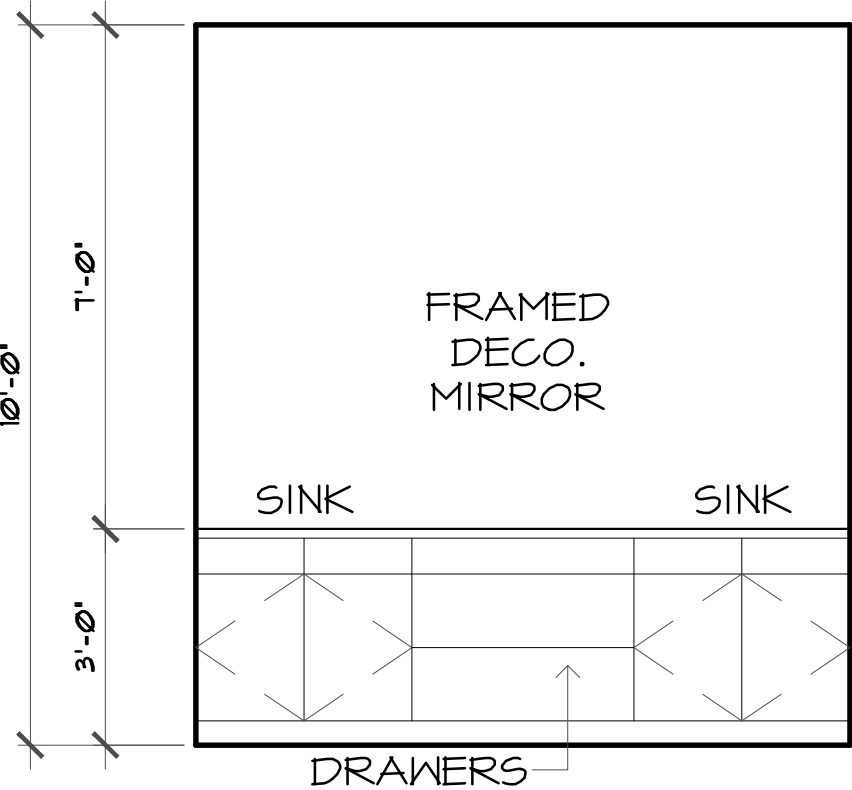


M. BA- VIEW A

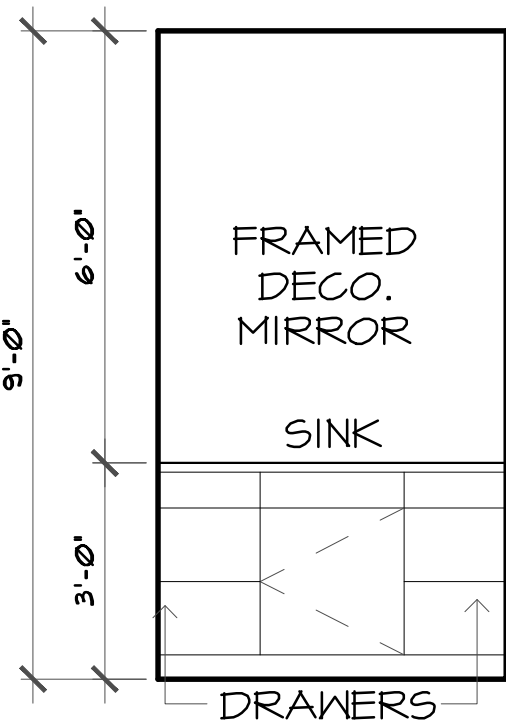


B.3 - VIEW D

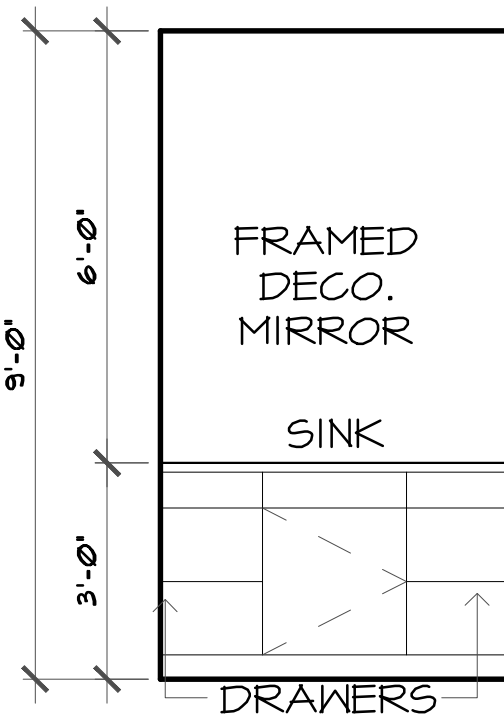


B.3 - VIEW B

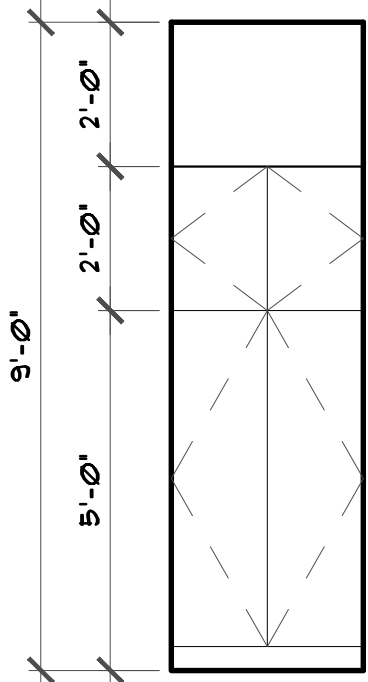

B.3 - VIEW A

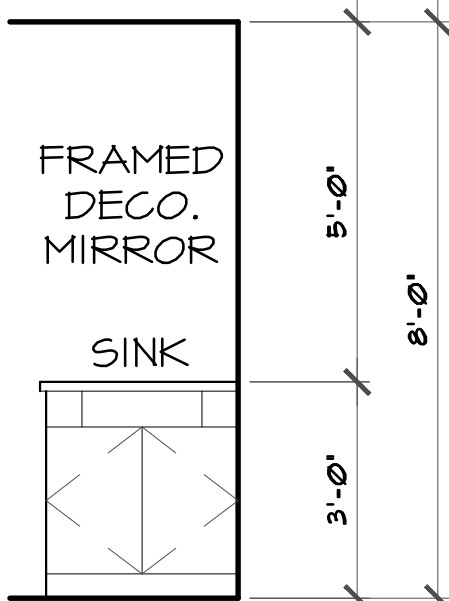

B.4- VIEW C

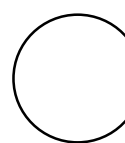


INTERIOR ELEVATIONS

3/8" = 1'-0"


REFER TO BOTTOM RIGHT HAND CORNER OF FLOOR PLANS FOR INTERIOR ELEVATION VIEW INDICATOR.

IF ANY WALL MOUNT FAUCETS ARE TO BE USED, VALVE HEIGHT MUST BE DETERMINED AT PLUMBING ROUGH

INTERIOR ELEVATIONS ARE CONCEPTUAL ONLY. CONFIRM LAYOUTS WITH BUILDER AND / OR CABINET SHOP DRAWINGS. MOULDINGS, MATERIAL, DOOR STYLE, ETC. TO BE DETERMINED BY OTHERS.

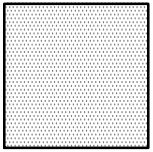

GLASS CABINET DOOR

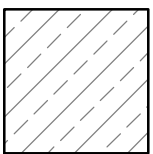

TILE - NOTE: THIS PATTERN IS USED FOR REPRESENTATIONAL PURPOSES ONLY. IT IS NOT INTENDED TO BE DIRECTION ON PATTERN OF TILE TO BE LAID.

REVISIONS


DATE	ITEM

JOB NUMBER 18-054

DATE 06-12-19

SCALE AS NOTED

DRAWN DC

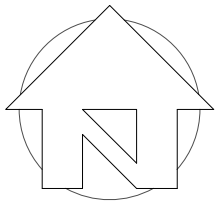

David Cox, cpbd

Houston, TX
832.604.6686 office
dcox@designdca.com
www.designdca.com



GARCIA/CABALLERO RESIDENCE

1ST FLOOR ELECTRICAL


1/4" = 1'-0"

NOTE: SMOKE ALARMS SHALL COMPLY WITH SECTION R313.2 (LOCATION) AND R313.3 (POWER SOURCE - HARD WIRED AND INTER-CONNECTED WITH BATTERY BACKUP)

SECTION: R315.1 CARBON MONOXIDE ALARMS. FOR NEW CONSTRUCTION, AN APPROVED CARBON MONOXIDE ALARM SHALL BE INSTALLED OUTSIDE OF EACH SEPARATE SLEEPING AREA IN THE IMMEDIATE VICINITY OF THE BEDROOMS IN DWELLING UNITS WITHIN WHICH FUEL-FIRED APPLIANCES ARE INSTALLED AND IN DWELLING UNITS THAT HAVE ATTACHED GARAGES. (COMBINED WITH SMOKE ALARM).


VERIFY LOW-VOLTAGE PRIOR TO CONSTRUCTION. IF PLANS EXIST FROM LOW-VOLTAGE SUBCONTRACTOR, IT TAKES PRECEDENCE.

ELECTRICAL LEGEND	
	110 VOLT RECEPTACLE
	WATERPROOF RECEPTACLE
	110 VOLT W/ GROUND FAULT INTERRUPTOR
	110 VOLT IN FLOOR
	220 VOLT RECEPTACLE
	RG 6 / 2 CAT 5
	SINGLE POLE SWITCH
	THREE WAY SWITCH
	FOUR WAY SWITCH
	DIMMER SWITCH
	PUSH BUTTON
	SMOKE DETECTOR
	SMOKE / CARBON MONOXIDE COMBO DETECTOR
	CEILING MOUNTED LIGHT FIXTURE
	CEILING MOUNTED HANGING LIGHT FIXTURE
	CEILING MOUNTED PENDANT LIGHT FIXTURE
	RECESSED CAN LIGHT
	RECESSED PIN SPOT LIGHT
	WATERPROOF RECESSED CAN LIGHT
	RECESSED EYEBALL SPOT LIGHT
	WALL MOUNTED LIGHT FIXTURE
	FLOOD LIGHTS
	EXHAUST FAN
	EXHAUST FAN / LIGHT COMBO
	U.S.B. OUTLET
	DOORBELL CHIMES
	UNDER UPPER CABINET LIGHTING- UNLESS OTHERWISE NOTED
	CEILING FAN
	CEILING FAN W/ LIGHT
	BLOCK AND WIRE FOR FAN WITH LIGHT
	FLUORESCENT LIGHT PANEL-SEE PLAN FOR SIZE

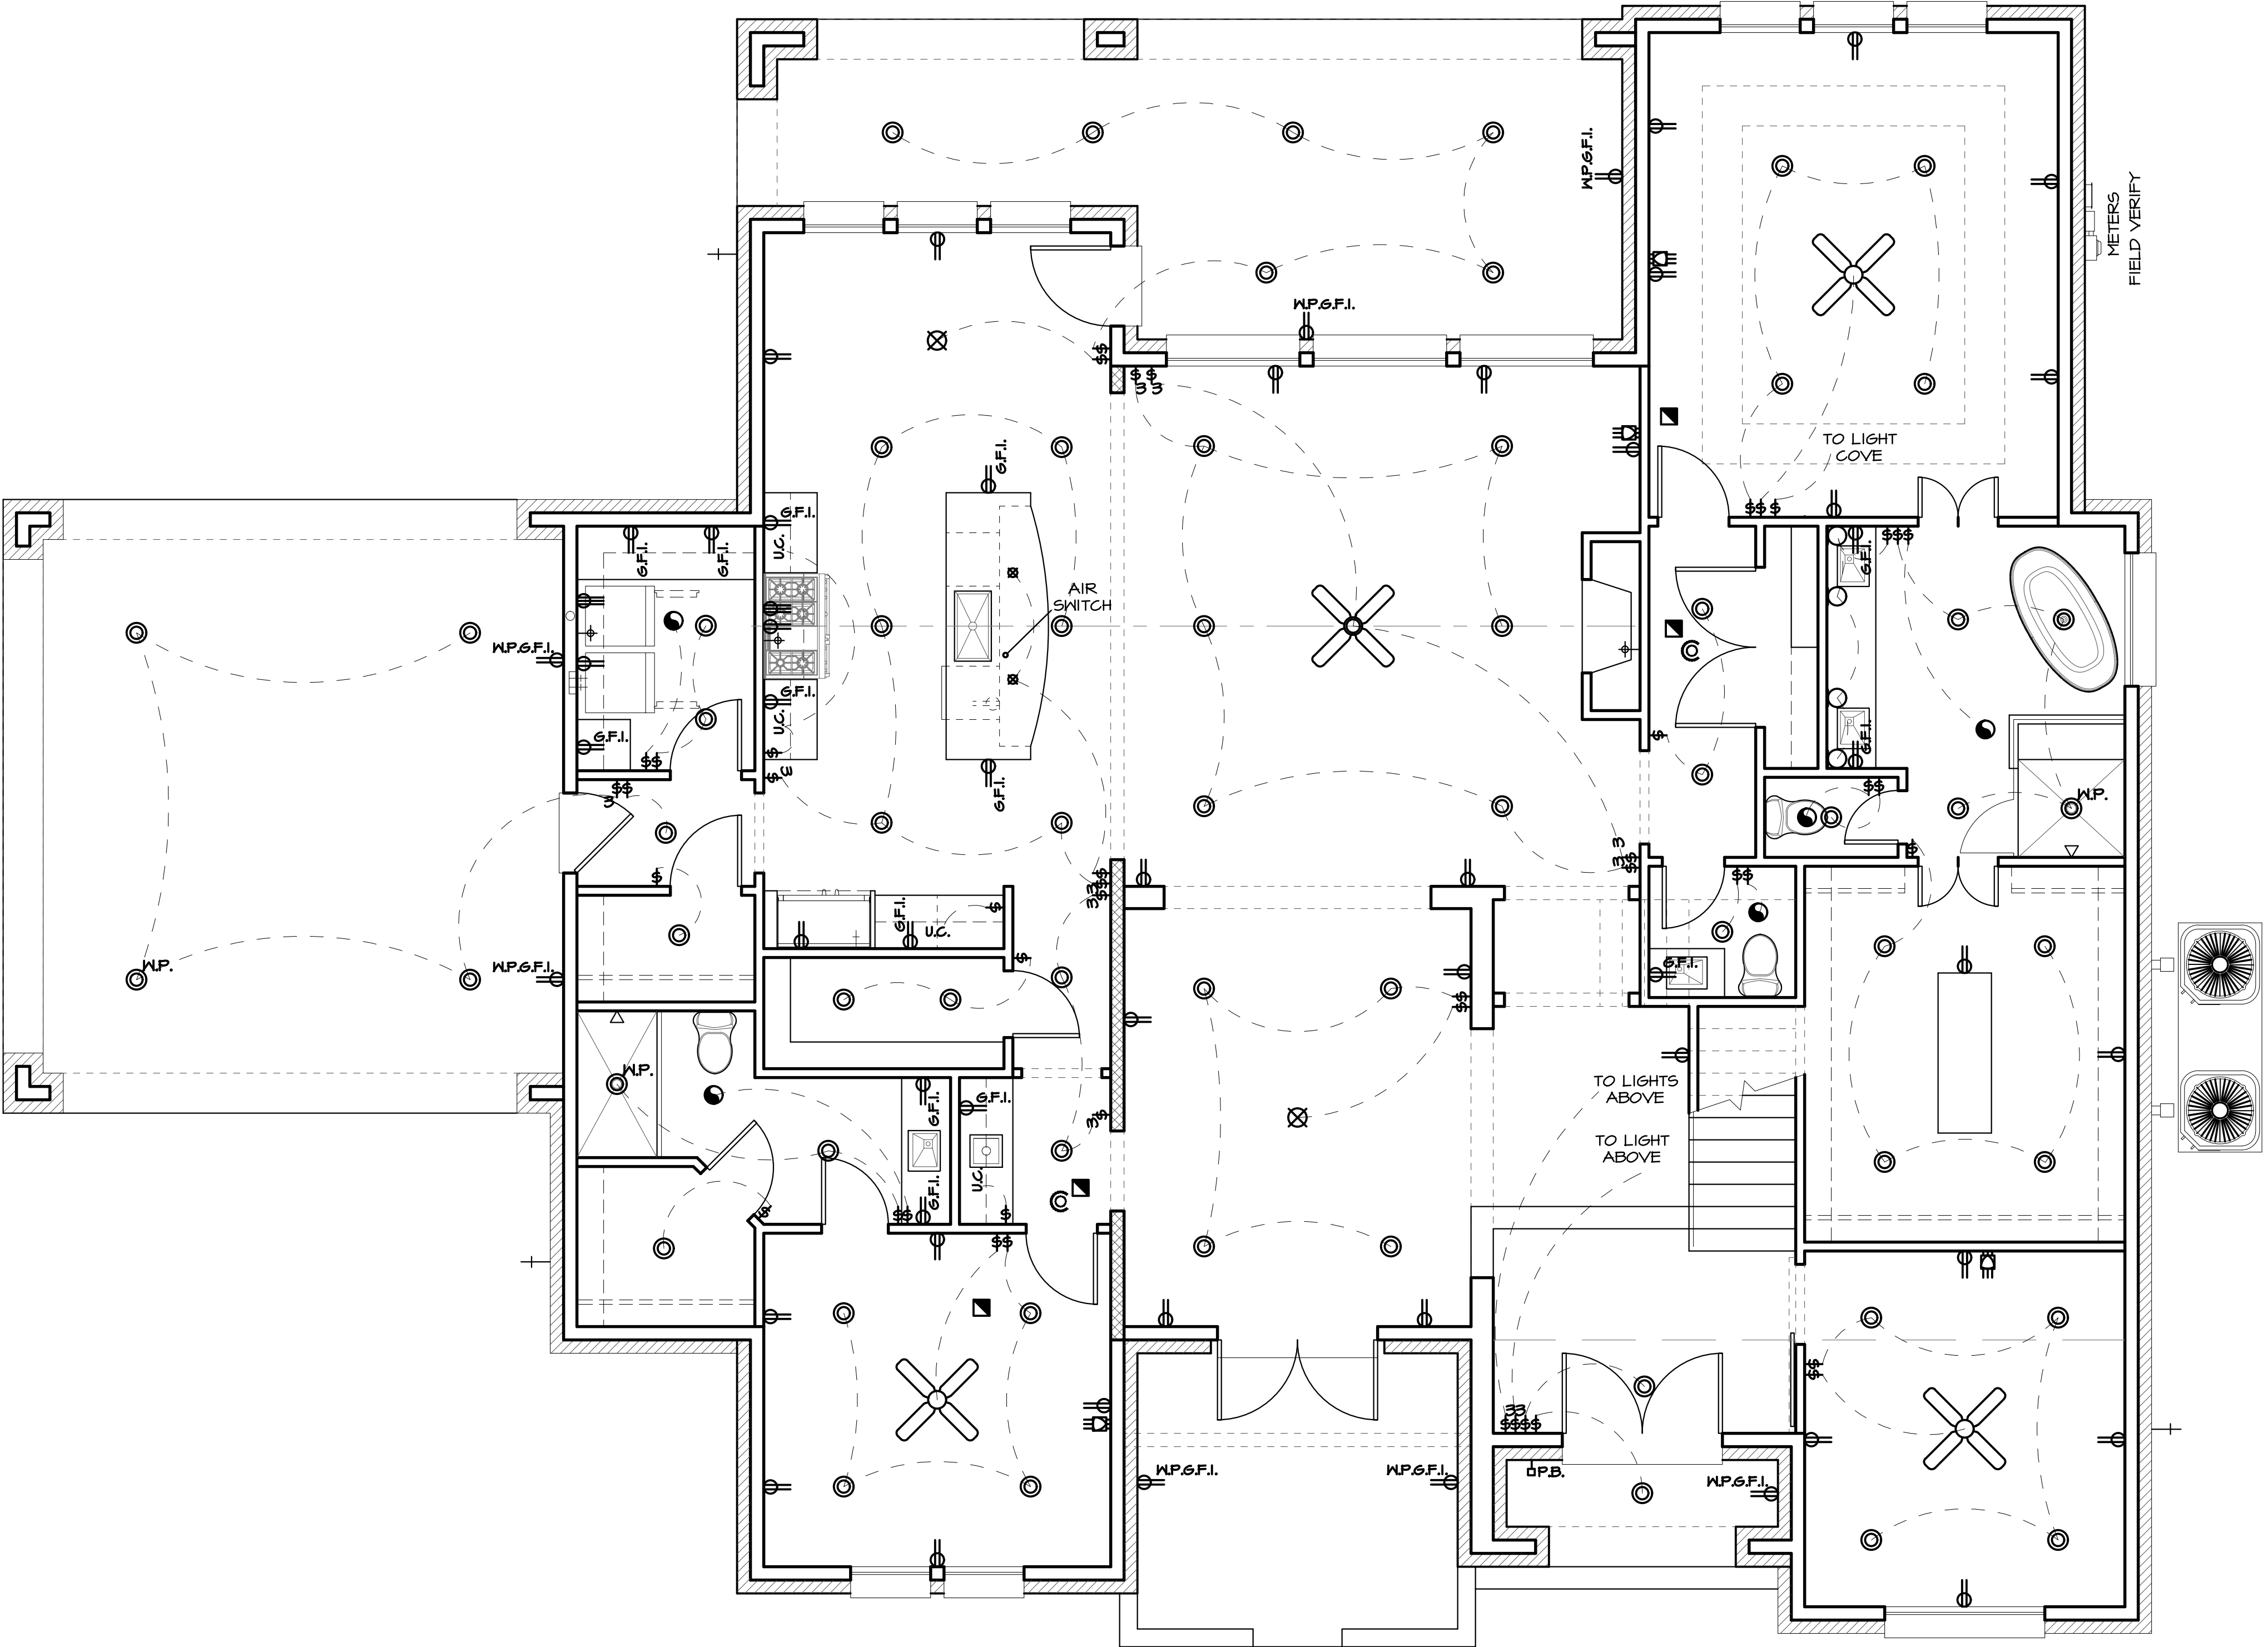

REVISIONS	
DATE	ITEM
JOB NUMBER	18-054
DATE	06-12-19
SCALE	AS NOTED
DRAWN	DC

E1

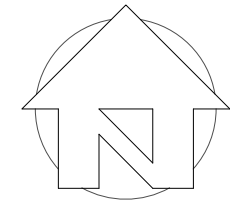

David Cox, cpbd

Houston, TX
832.604.6686 office
dcox@designdca.com
www.designdca.com



GARCIA/CABALLERO RESIDENCE

2ND FLOOR ELECTRICAL

1/4" = 1'-0"

NOTE: SMOKE ALARMS SHALL COMPLY WITH SECTION R313.2 (LOCATION) AND R313.3 (POWER SOURCE - HARD WIRED AND INTER-CONNECTED WITH BATTERY BACKUP)

SECTION: R315.1 CARBON MONOXIDE ALARMS. FOR NEW CONSTRUCTION, AN APPROVED CARBON MONOXIDE ALARM SHALL BE INSTALLED OUTSIDE OF EACH SEPARATE SLEEPING AREA IN THE IMMEDIATE VICINITY OF THE BEDROOMS IN DWELLING UNITS WITHIN WHICH FUEL-FIRED APPLIANCES ARE INSTALLED AND IN DWELLING UNITS THAT HAVE ATTACHED GARAGES. (COMBINED WITH SMOKE ALARM).

VERIFY LOW-VOLTAGE PRIOR TO CONSTRUCTION. IF PLANS EXIST FROM LOW-VOLTAGE SUBCONTRACTOR, IT TAKES PRECEDENCE.

ELECTRICAL LEGEND

	110 VOLT RECEPTACLE
	WATERPROOF RECEPTACLE
	110 VOLT W/ GROUND FAULT INTERRUPTOR
	110 VOLT IN FLOOR
	220 VOLT RECEPTACLE
	RG 6/ 2 CAT 5
	SINGLE POLE SWITCH
	THREE WAY SWITCH
	FOUR WAY SWITCH
	DIMMER SWITCH
	PUSH BUTTON
	SMOKE DETECTOR
	SMOKE / CARBON MONOXIDE COMBO DETECTOR
	CEILING MOUNTED LIGHT FIXTURE
	CEILING MOUNTED HANGING LIGHT FIXTURE
	CEILING MOUNTED PENDANT LIGHT FIXTURE
	RECESSED CAN LIGHT
	RECESSED PIN SPOT LIGHT
	WATERPROOF RECESSED CAN LIGHT
	RECESSED EYEBALL SPOT LIGHT
	WALL MOUNTED LIGHT FIXTURE
	FLOOD LIGHTS
	EXHAUST FAN
	EXHAUST FAN / LIGHT COMBO
	U.S.B. OUTLET
	DOORBELL CHIMES
	UNDER UPPER CABINET LIGHTING- UNLESS OTHERWISE NOTED
	CEILING FAN
	CEILING FAN W/ LIGHT
	BLOCK AND WIRE FOR FAN WITH LIGHT
	FLUORESCENT LIGHT PANEL-SEE PLAN FOR SIZE

